
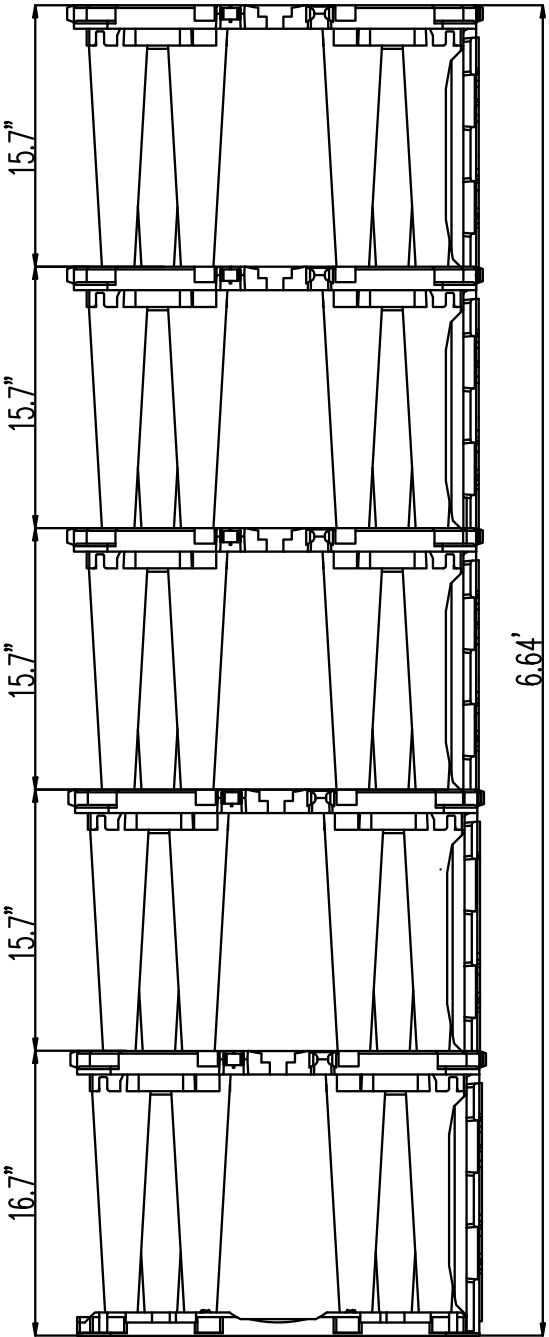
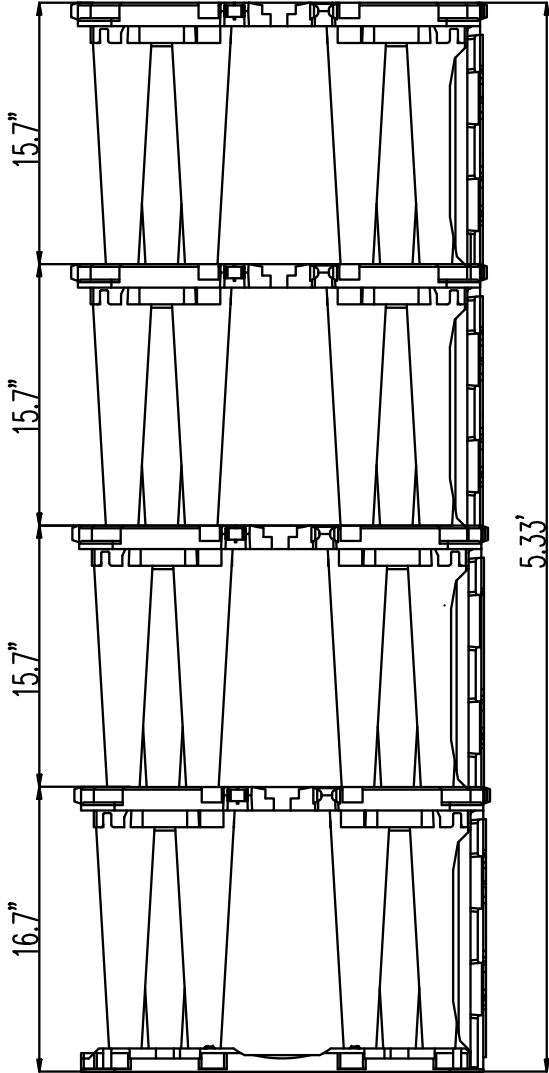
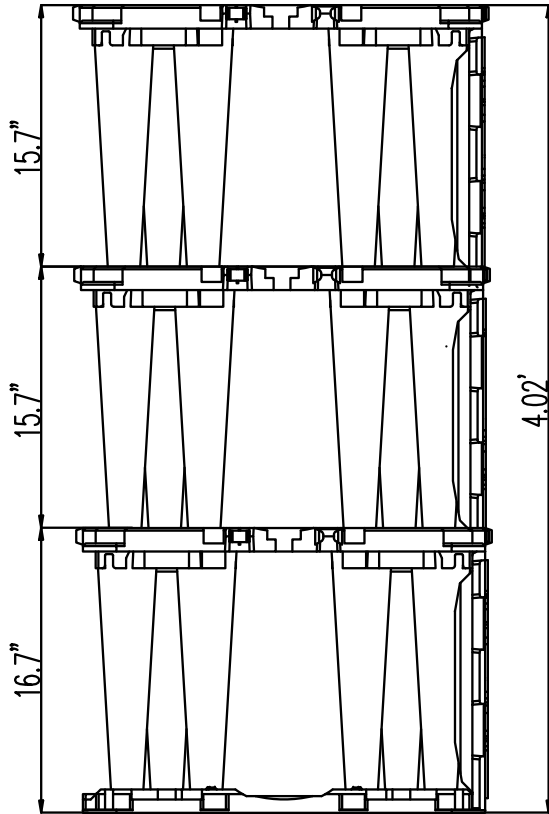
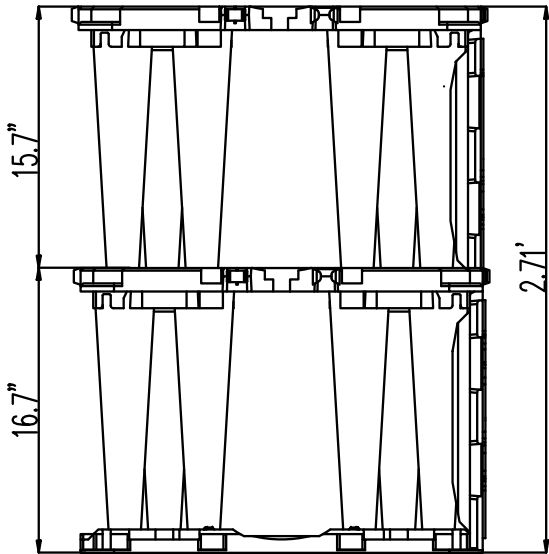


AquaCell Crate + bottom +1 side plate	# Layers	Height of layers (ft)	Volume water (ft³)	Gross Volume total (ft³)	Percentage water
SD 1.0	1	1.4	10.2	10.8	94%
SD 2.0	2	2.7	19.8	21.0	95%
SD 3.0	3	4.0	29.5	31.1	95%
SD 4.0	4	5.3	39.2	41.3	95%
SD 5.0	5	6.6	48.8	51.5	95%
SD 6.0	6	8.0	58.5	61.7	95%
SD 7.0	7	9.3	68.2	71.8	95%
SD 8.0	8	10.6	77.8	82.0	95%

AquaCell Crate + bottom + 2 side plates	# Layers	Height of layers (ft)	Volume water (ft³)	Gross Volume total (ft³)	Percentage water
SD 1.0	1	1.4	10.1	10.8	93%
SD 2.0	2	2.7	19.7	21.0	94%
SD 3.0	3	4.0	29.3	31.1	94%
SD 4.0	4	5.3	38.8	41.3	94%
SD 5.0	5	6.6	48.4	51.5	94%
SD 6.0	6	8.0	58.0	61.7	94%
SD 7.0	7	9.3	67.6	71.8	94%
SD 8.0	8	10.6	77.2	82.0	94%

AquaCell Crate with bottom plate (1st Layer Only)	# Layers	Height of layers (ft)	Water Volume (ft³)	Total Crate Volume (ft³)	Percentage water
SD 1.0	1	1.4	10.3	10.8	95%
SD 2.0	2	2.7	20.0	21.0	95%
SD 3.0	3	4.0	29.7	31.1	95%
SD 4.0	4	5.3	39.5	41.3	96%
SD 5.0	5	6.6	49.2	51.5	96%
SD 6.0	6	8.0	59.0	61.7	96%
SD 7.0	7	9.3	68.7	71.8	96%
SD 8.0	8	10.6	78.5	82.0	96%

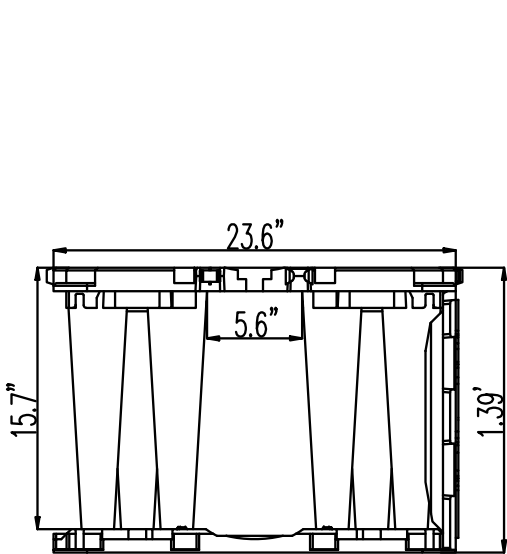

*maximum total of 8 layers stacked

NOTES:

1. Volume of designed water storage is an average of 95% of total volume of water stored within the AquaCell units
2. AquaCell units can be stacked to a maximum of eight (8) layers for an underground stormwater retention / detention system.
3. Water storage values shown represent one type of configuration. Additional side plates added will reduce percentage of water volume by an average of -.8% per layer.
4. Extra Strong AquaCell configuration (2 base units set within each other) has a water volume of 11.7 ft³ with 10.8 ft³ of designed water storage.



Managing water better since 1955.
 950 Winter Street
 Waltham, MA 02451
 wavin.us.com
 wavintechsupport@orbia.com

Title: AquaCell 5-Layer Stack w. Measurements

The design details/specifications presented in this document are for informational & reference purposes only and are subject to change without notice. Responsibility for design of any AquaCell system rests solely with the original design engineer of record. For questions, contact: wavintechsupport@orbia.com.	Drawn by: HJD	Approved by: KS	Sheet 1 of 1
	Scale: 1:11	Revision: 2	
	AQ-100-05	Date: 2/23/2025	