


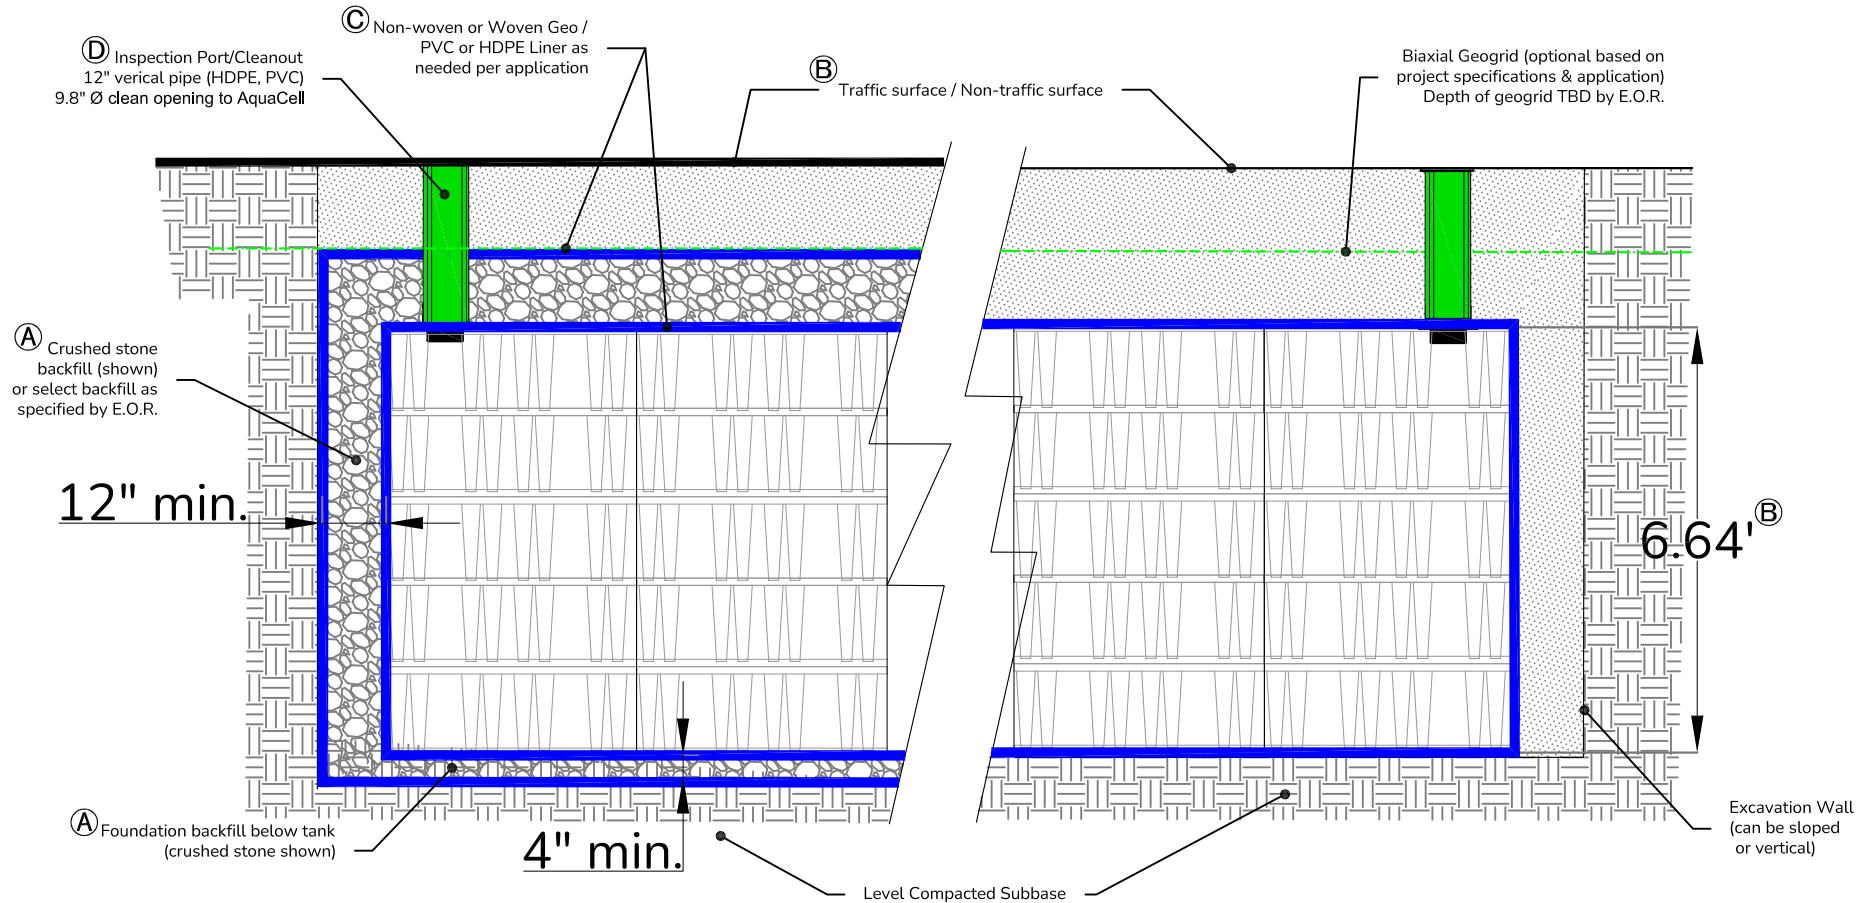

Notes:

- ① Minimum backfill requirements noted for reference: 4" foundation backfill & 12" perimeter backfill.
- ② Reference Installation Depth Requirements (AQ-100-02) for minimum top cover traffic load depths and compaction requirements.
- ③ Reference Geosynthetics Detail (AQ-100-03.1 & AQ-100-03.2) for minimum material weights and application details.
- ④ Reference AquaCell Installation Guide for further information and instruction on vertical & horizontal pipe connections.



Managing water better since 1955.
 950 Winter Street
 Waltham, MA 02451
 wavin.us
 wavintechsupport@orbia.com



The design details/specifications presented in this document are for informational purposes only and are subject to change without notice. Responsibility for design of any AquaCell system rests solely with the original design engineer of record. For questions, contact:
 wavintechsupport@orbia.com

Title: AquaCell SC-5 Layer Cross Section			
Date: 12/1/25	Scale: NTS	Rev #: 2	Sheet: 1 of 1
Drawn: HJD	Approved: JBS	Drawing #: AQ-100-15	