


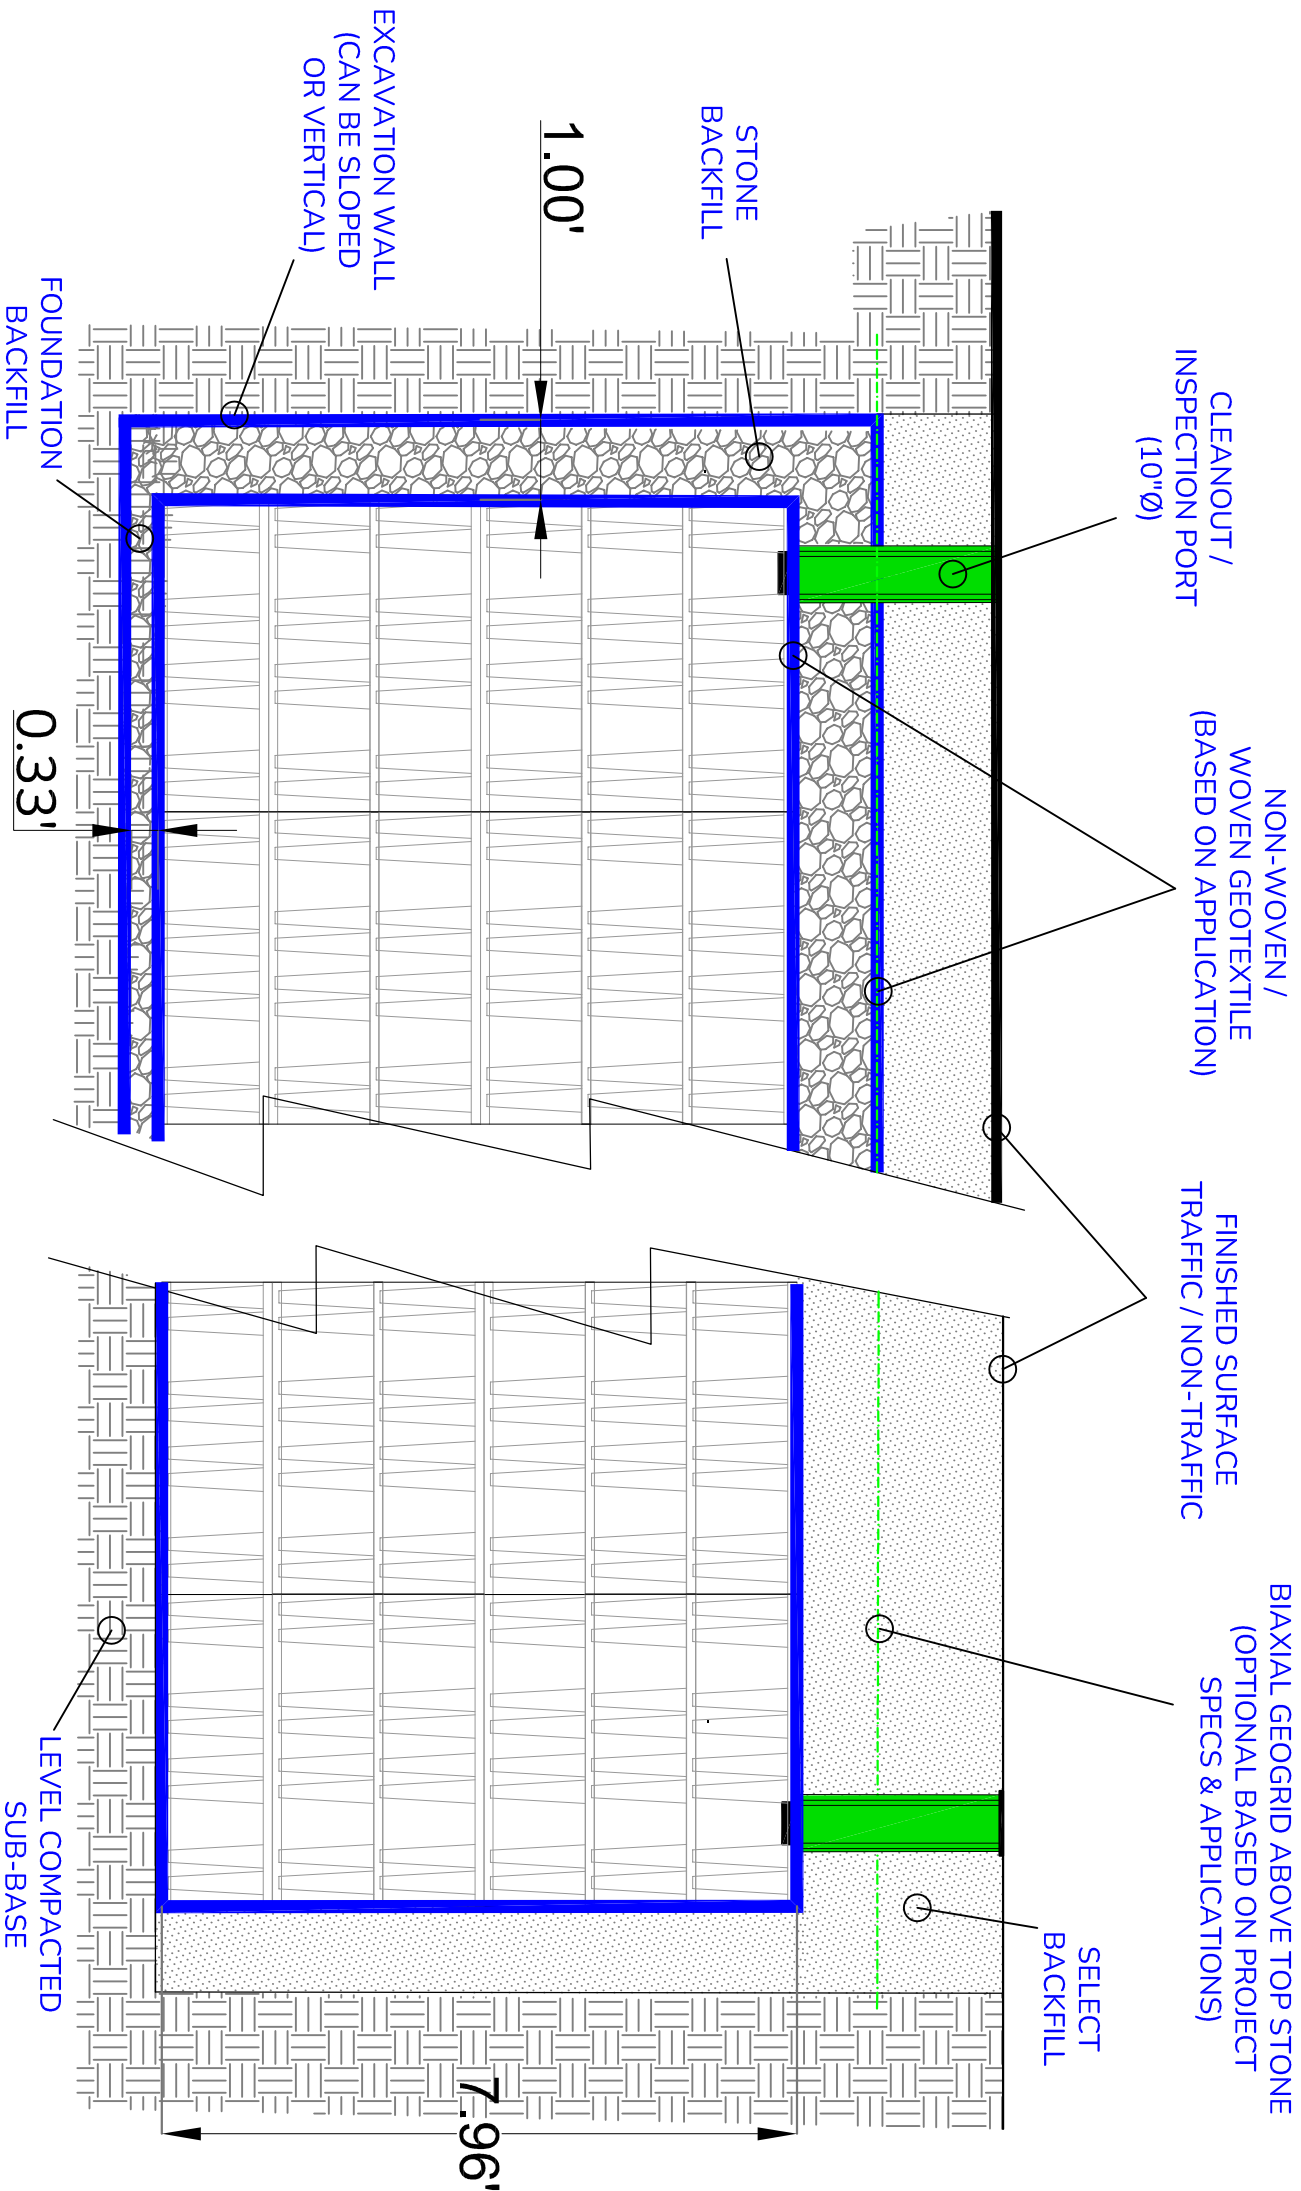

Notes:

1. Minimum backfill requirements noted for reference: **4" (0.33') foundation backfill & 12" (1.0') perimeter backfill.**
2. Reference Installation **Depth Requirements (AQ-100-02)** for top cover load depths and compaction requirements.
3. Reference **Geosynthetics Detail (AQ-100-03)** for minimum material weights and application details.
4. Reference **AquaCell Installation Guide** for further information and instruction on vertical & horizontal pipe connections.



Managing water better since 1955.
950 Winter Street
Waltham, MA 02451
wavin.us
wavintechsupport@orbia.com



The design details/specifications presented in this document are for informational purposes only and are subject to change without notice. Responsibility for design of any AquaCell system rests solely with the original design engineer of record. For questions, contact: wavintechsupport@orbia.com

Title: AquaCell SD-6 Layer Cross Section				
Date: 4/23/2025	Scale: NTS	Drawing: AQ-100-16	Rev: 1	
Drawn: HJD	Approved:	Sheet: 1 of 1		