


AquaCell Crate (2 Base Units)	# Layers	Height of Layers (ft)	Total Crate Volume (ft³)	Water Volume (ft³)	Percentage Water
EX 1.0	1	1.51	11.7	10.8	93%
EX 2.0	2	3.02	23.4	22.1	94%
EX 3.0	3	4.53	35.1	33.4	95%
EX 4.0	4	6.04	46.8	44.6	95%
EX 5.0	5	7.55	58.5	55.9	96%
EX 6.0	6	9.06	70.2	67.2	96%
EX 7.0	7	10.56	81.9	78.5	96%
EX 8.0	8	12.07	93.6	89.7	96%

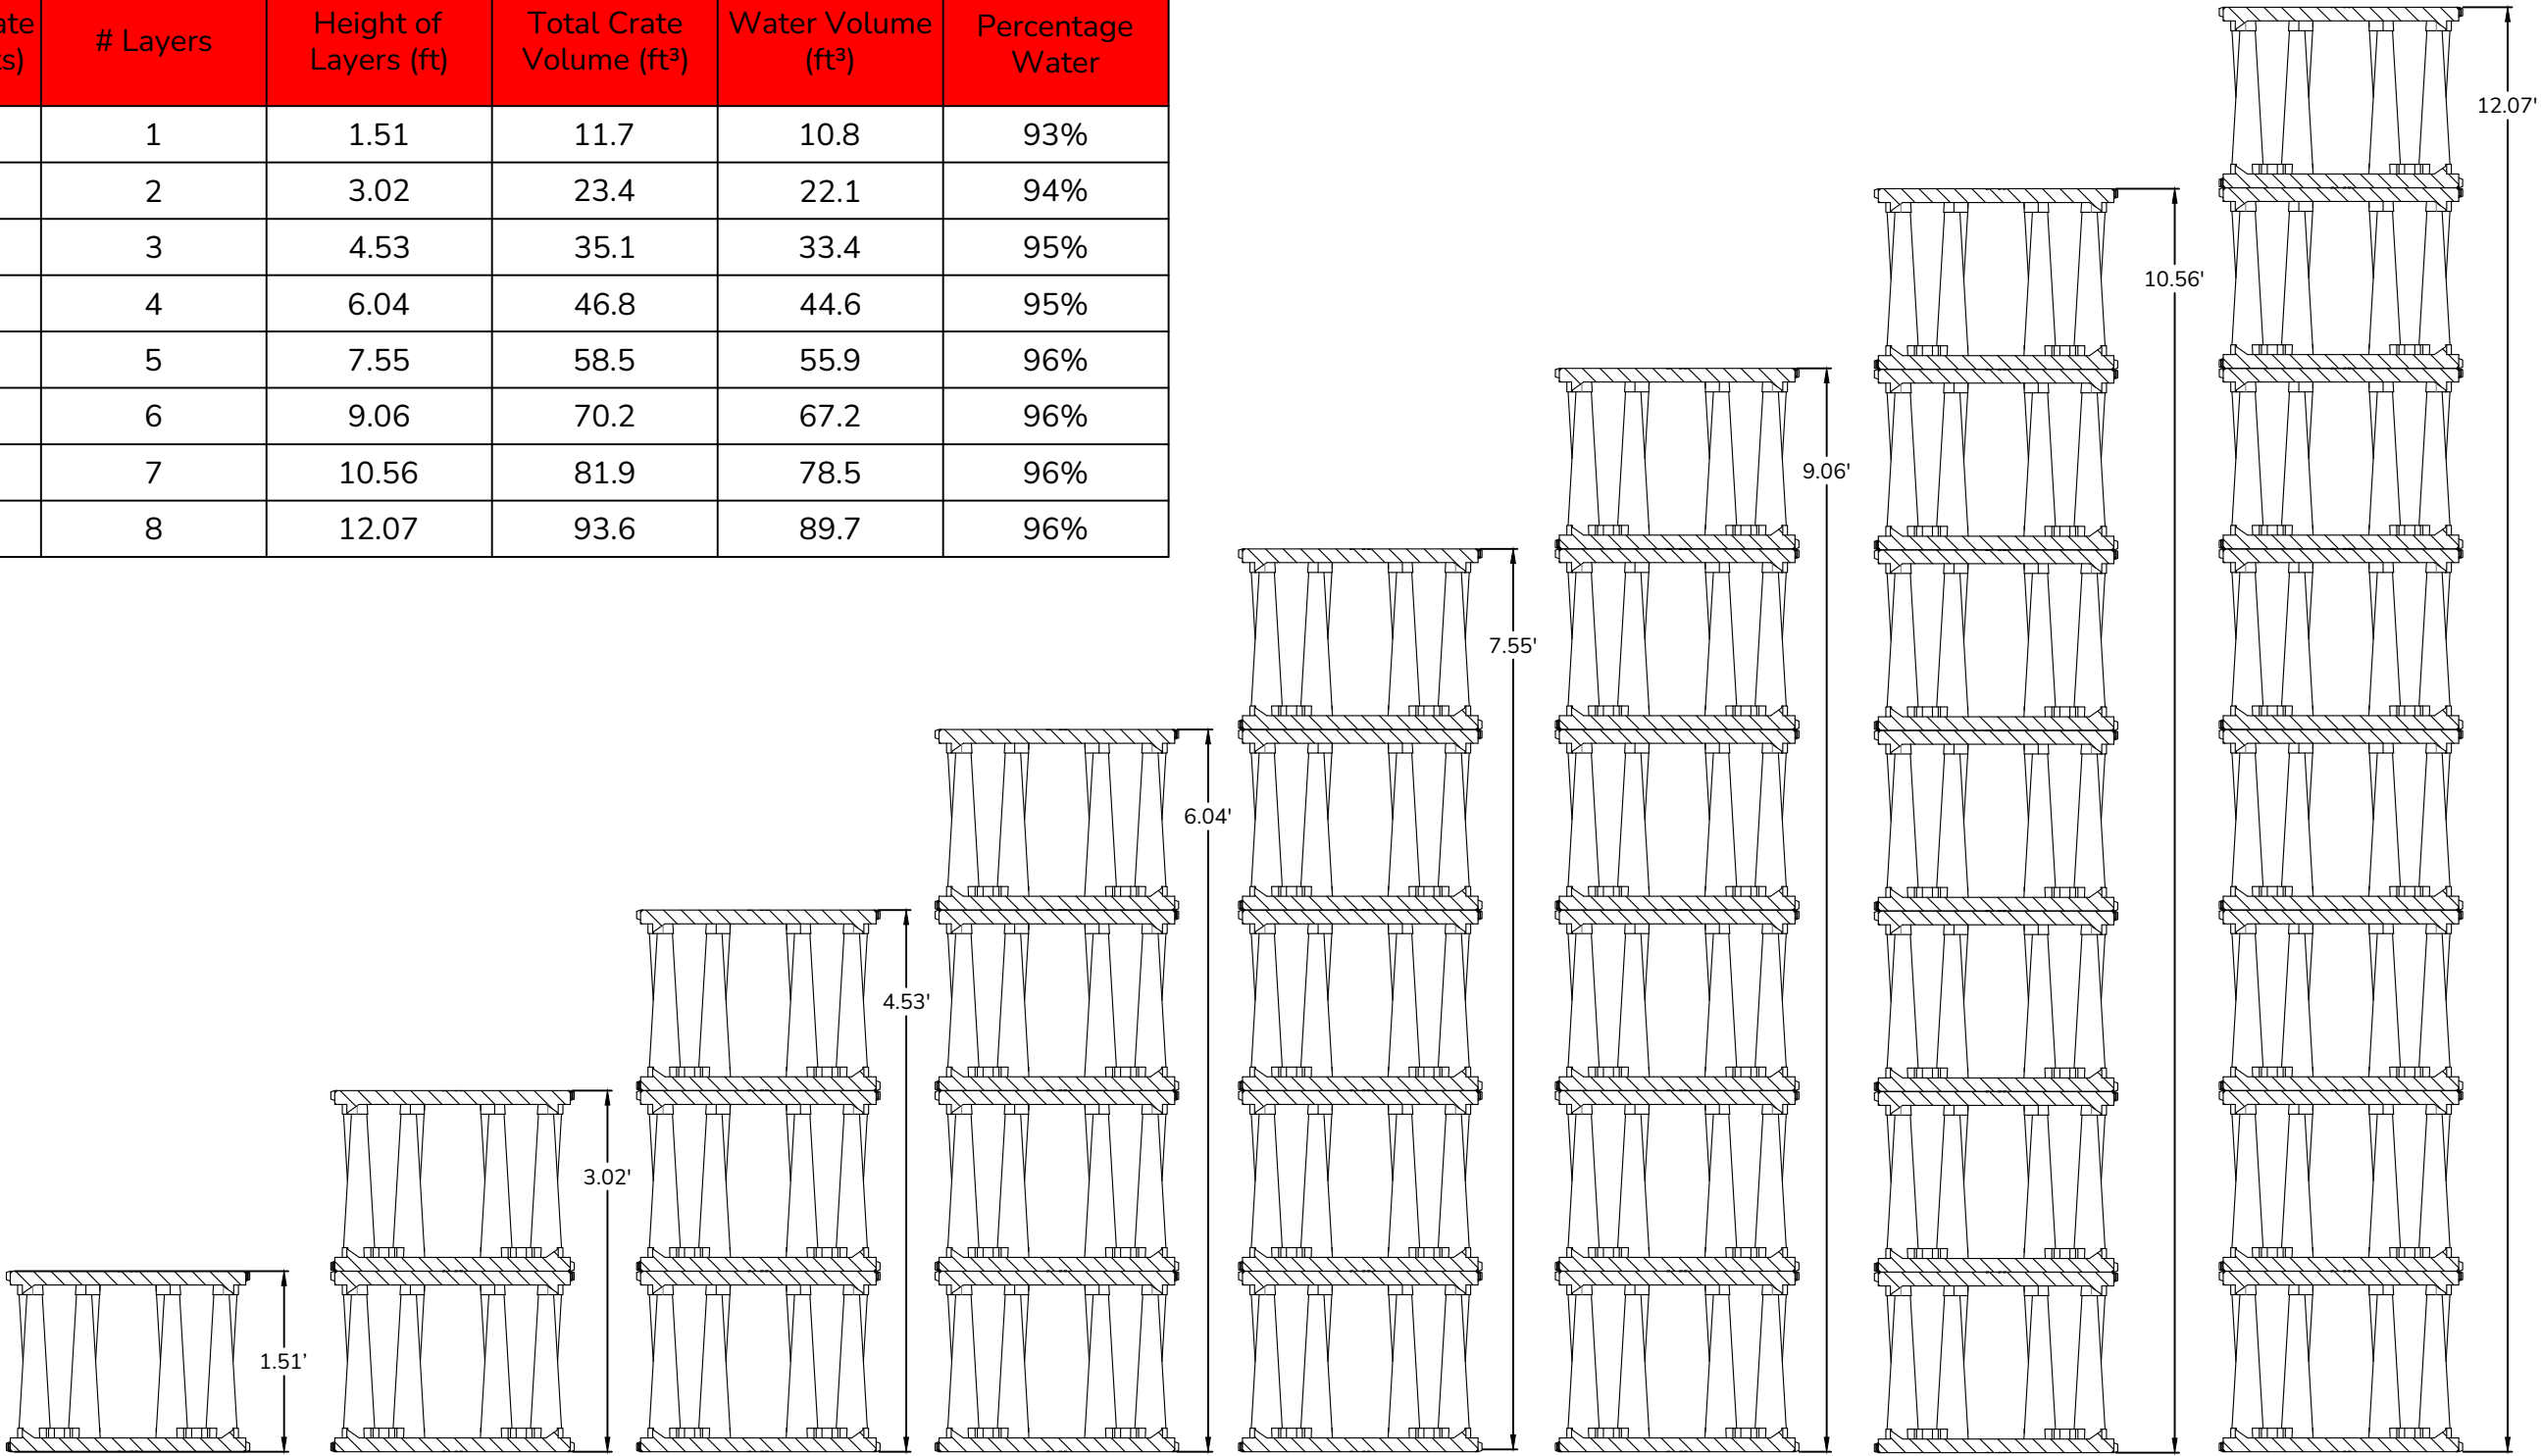

Managing water better since 1955.
950 Winter Street
Waltham, MA 02451
wavin.us
wavintechsupport@orbia.com



The design details/specifications presented in this document are for informational purposes only and are subject to change without notice. Responsibility for design of any AquaCell system rests solely with the original design engineer of record. For questions, contact: wavintechsupport@orbia.com

Title: AquaCell Extra Strong (EX) Crate Measurements			
Date: 3/7/2025	Scale: NTS	Rev: 0	
Drawn: HJD	Approved: JS	Drawing: AQ-100-23	