


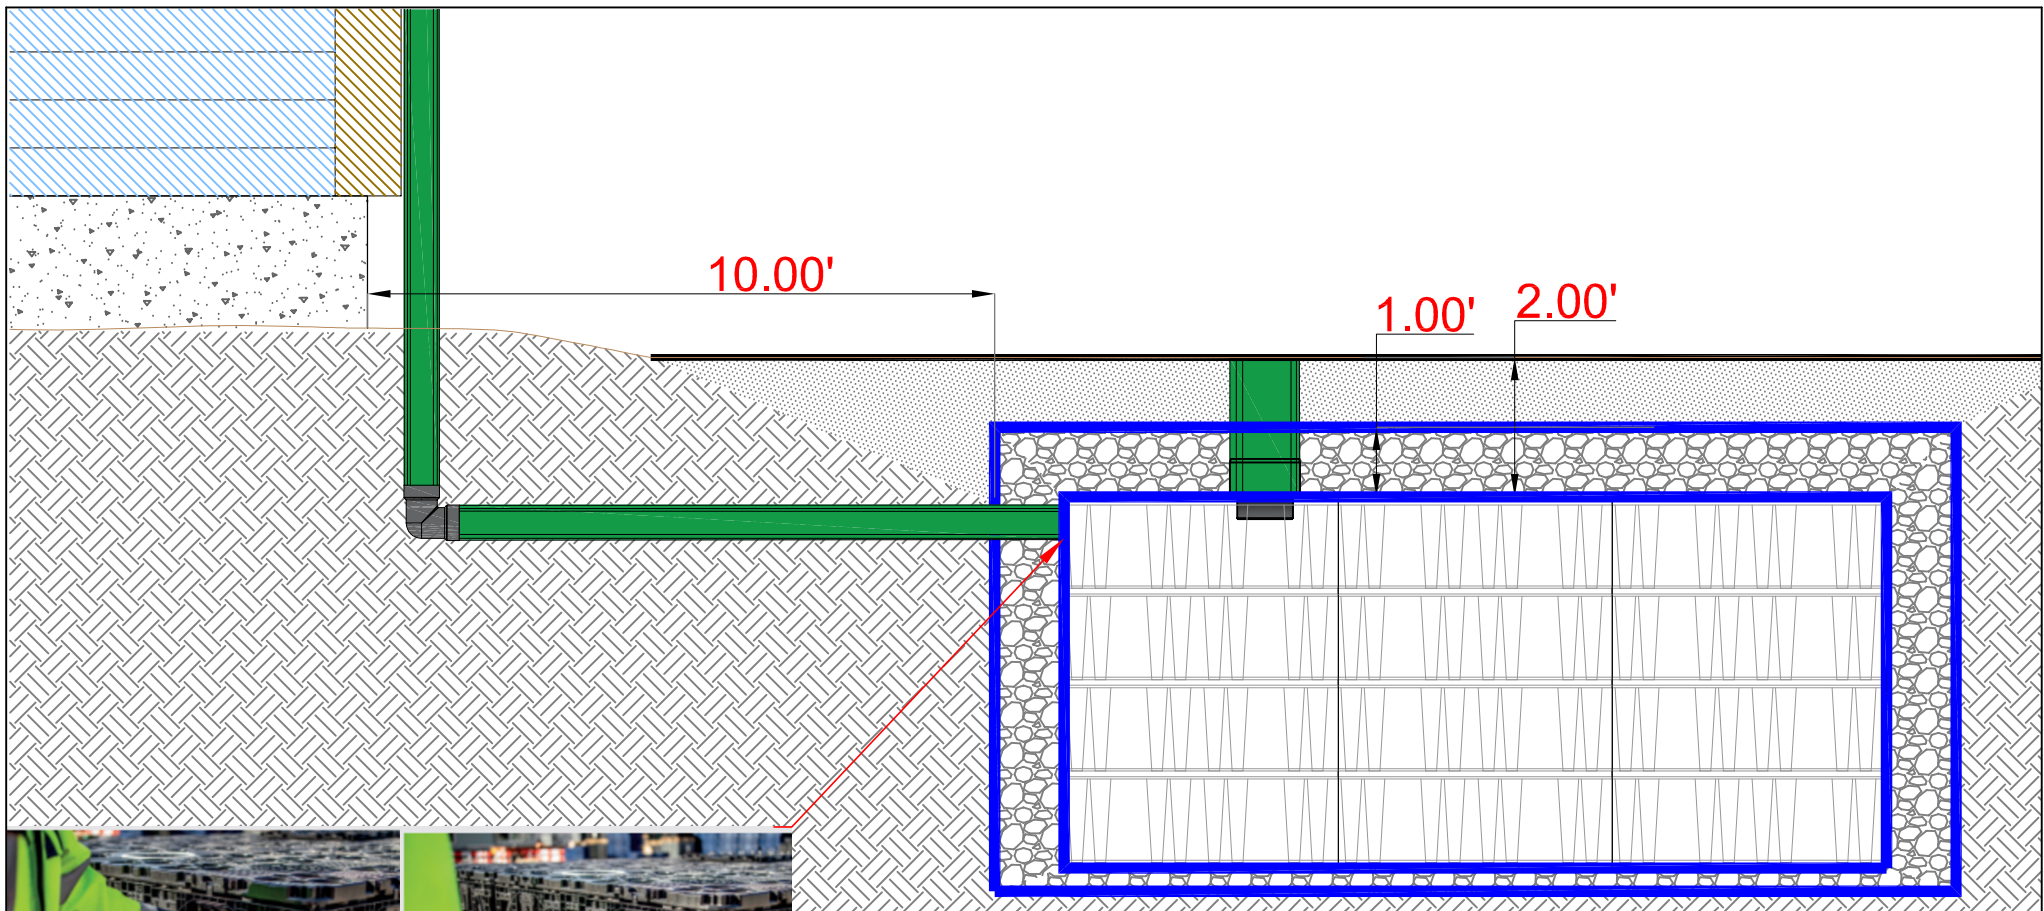

Notes:

1. For roof drain connection using PVC SDR 26[35 (ASTM D3034) 6.4" OD diameter or less, connect directly to AquaCell side panels via standard 6" with integrated pipe stopper.
2. Reference **AQ-100-22 Six-inch PVC Pipe to AquaCell Side Panel Detail** for further installation guidance and on completing geotextile wrap around the 6" side panel connections.
3. Reference **AquaCell Installation Guide** for further information and instructions related to AquaCell Top Adapter, vertical pipe, minimum surface to top of tank distances, and geosynthetics installation.
4. AquaCell is not intended to support structural loads from buildings, retaining walls, or other load-bearing structures. When depth of structural elements are not known, a minimum distance of 10 feet from the base of the structure to the edge of the perimeter stone is required.



Managing water better since 1955.
 950 Winter Street
 Waltham, MA 02451
 wavin.us
 wavintechsupport@orbia.com

WAVIN.US



The design details/specifications presented in this document are for informational purposes only and are subject to change without notice. Responsibility for design of any AquaCell system rests solely with the original design engineer of record. For questions, contact: wavintechsupport@orbia.com

Title: Roof Drain Connection to AquaCell			
Date: 8/4/2025	Scale: NTS	Drawing: AQ-100-26	Rev: 0
Drawn: HJD	Approved: JS	Sheet: 1 of 1	