
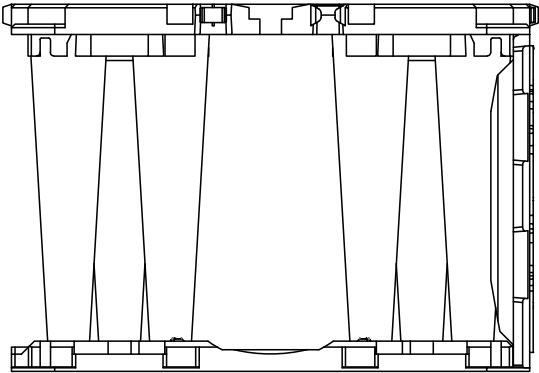
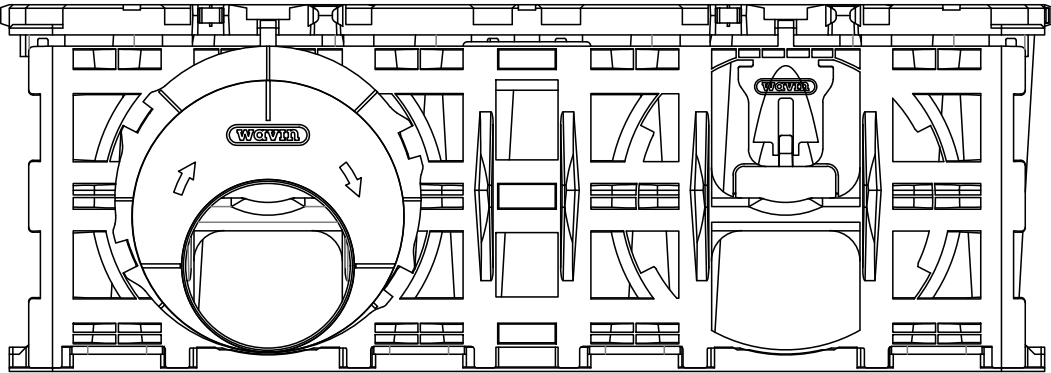


| AquaCell Crate With Bottom Plate<br>(1st Layer Only) | # Layers | Height of Layers (ft) | Height of Layers (in) | Water Volume (ft³) | Total Crate Volume (ft³) | Percentage Water |
|------------------------------------------------------|----------|-----------------------|-----------------------|--------------------|--------------------------|------------------|
| SC-1                                                 | 1        | 1.39                  | 16.73                 | 10.25              | 10.81                    | 94.87%           |
| SC-2                                                 | 2        | 2.71                  | 32.48                 | 20.0               | 20.98                    | 95.33%           |
| SC-3                                                 | 3        | 4.02                  | 48.23                 | 29.7               | 31.15                    | 95.49%           |
| SC-4                                                 | 4        | 5.33                  | 63.98                 | 39.5               | 41.32                    | 95.57%           |
| SC-5                                                 | 5        | 6.64                  | 79.72                 | 49.2               | 51.49                    | 95.62%           |
| SC-6                                                 | 6        | 7.96                  | 95.47                 | 59.0               | 61.66                    | 95.65%           |
| SC-7                                                 | 7        | 9.27                  | 111.22                | 68.7               | 71.83                    | 95.67%           |
| SC-8                                                 | 8        | 10.58                 | 126.97                | 78.5               | 82.00                    | 95.69%           |

| AquaCell Crate + Bottom +1 Side Plate | # Layers | Height of Layers (ft) | Height of Layers (in) | Water Volume (ft³) | Gross Volume total (ft³) | Percentage Water |
|---------------------------------------|----------|-----------------------|-----------------------|--------------------|--------------------------|------------------|
| SC-1                                  | 1        | 1.39                  | 16.73                 | 10.17              | 10.81                    | 94.13%           |
| SC-2                                  | 2        | 2.71                  | 32.48                 | 19.84              | 20.98                    | 94.57%           |
| SC-3                                  | 3        | 4.02                  | 48.23                 | 29.50              | 31.15                    | 94.72%           |
| SC-4                                  | 4        | 5.33                  | 63.98                 | 39.17              | 41.32                    | 94.79%           |
| SC-5                                  | 5        | 6.64                  | 79.72                 | 48.83              | 51.49                    | 94.84%           |
| SC-6                                  | 6        | 7.96                  | 95.47                 | 58.50              | 61.66                    | 94.87%           |
| SC-7                                  | 7        | 9.27                  | 111.22                | 68.16              | 71.83                    | 94.90%           |
| SC-8                                  | 8        | 10.58                 | 126.97                | 77.83              | 82.00                    | 94.91%           |

| AquaCell Crate + Bottom + 2 Side Plates | # Layers | Height of Layers (ft) | Height of Layers (in) | Water Volume (ft³) | Gross Volume total (ft³) | Percentage Water |
|-----------------------------------------|----------|-----------------------|-----------------------|--------------------|--------------------------|------------------|
| SC-1                                    | 1        | 1.39                  | 16.73                 | 10.09              | 10.81                    | 93.39%           |
| SC-2                                    | 2        | 2.71                  | 32.48                 | 19.68              | 20.98                    | 93.80%           |
| SC-3                                    | 3        | 4.02                  | 48.23                 | 29.26              | 31.15                    | 93.95%           |
| SC-4                                    | 4        | 5.33                  | 63.98                 | 38.85              | 41.32                    | 94.02%           |
| SC-5                                    | 5        | 6.64                  | 79.72                 | 48.43              | 51.49                    | 94.07%           |
| SC-6                                    | 6        | 7.96                  | 95.47                 | 58.02              | 61.66                    | 94.10%           |
| SC-7                                    | 7        | 9.27                  | 111.22                | 67.60              | 71.83                    | 94.12%           |
| SC-8                                    | 8        | 10.58                 | 126.97                | 77.19              | 82.00                    | 94.13%           |

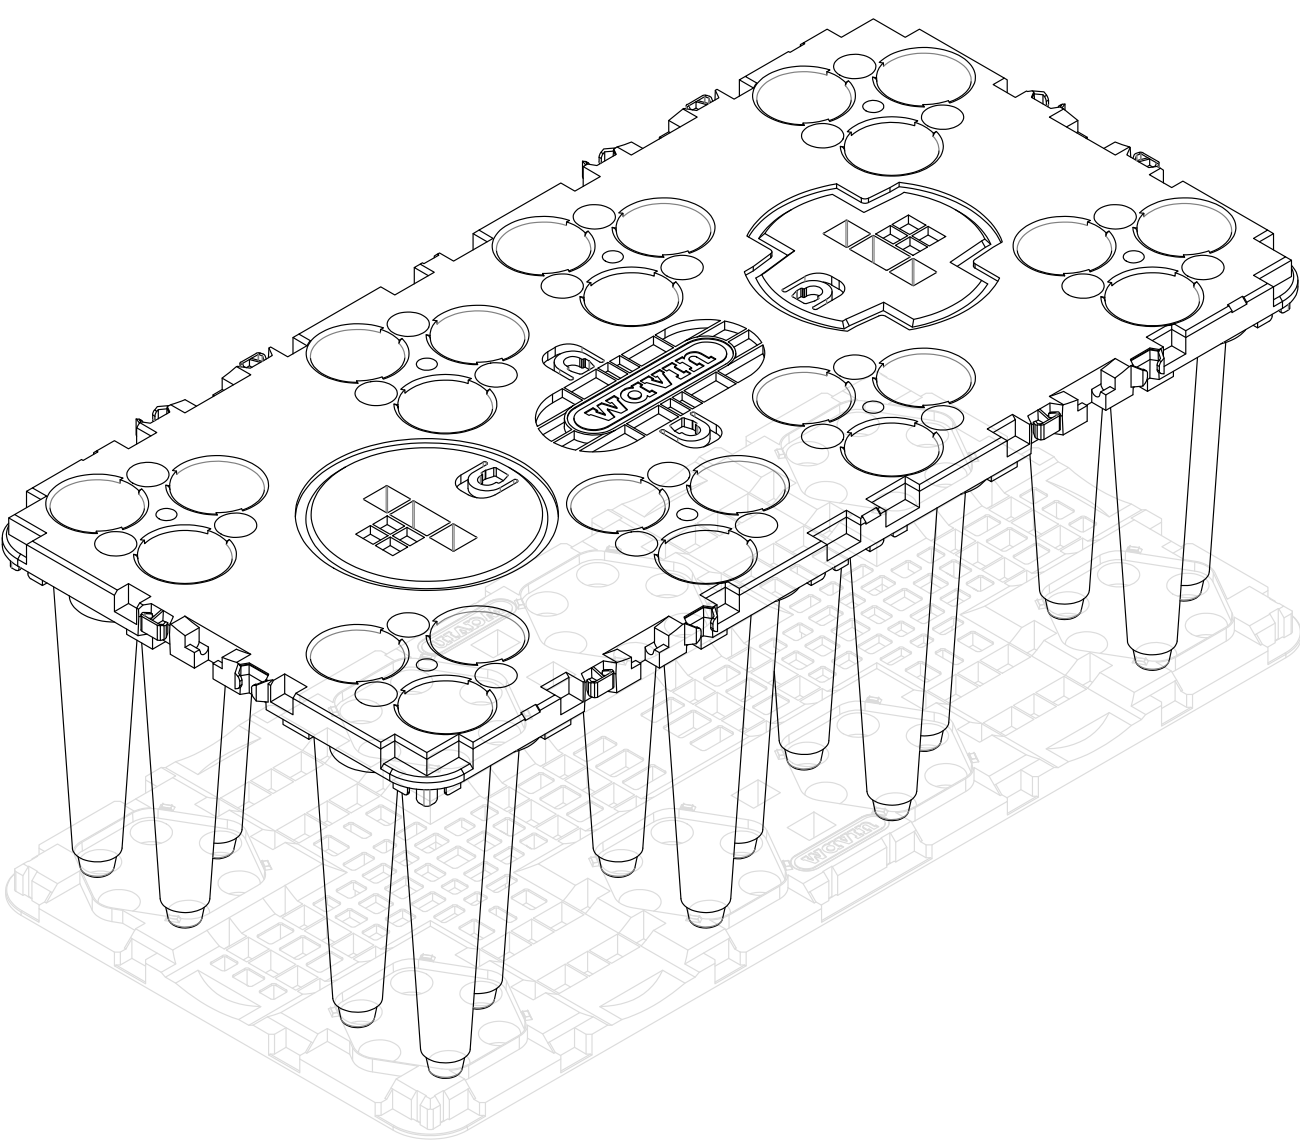

Managing water better since 1955.  
950 Winter Street  
Waltham, MA 02451  
wavin.us.com  
wavintechsupport@orbia.com

Title: AquaCell Volume Calculations - Standard (SC) Configuration



The design details/specifications presented in this document are for informational & reference purposes only and are subject to change without notice. Responsibility for design of any AquaCell system rests solely with the original design engineer of record. For questions, contact: wavintechsupport@orbia.com.

|               |                 |
|---------------|-----------------|
| Drawn by: HJD | Approved by: KS |
| Scale: NTS    | Revision: 4     |
| AQ-200-01     | Date: 11/10/25  |

| AquaCell Crate +<br>(2 Base Units) | # Layers | Height of<br>layers (ft) | Height of<br>Layers (in) | Water Volume<br>(ft³) | Total Crate<br>Volume (ft³) | Percentage<br>water |
|------------------------------------|----------|--------------------------|--------------------------|-----------------------|-----------------------------|---------------------|
| EX-1                               | 1        | 1.51                     | 18.11                    | 10.83                 | 11.70                       | 92.63%              |
| EX-2                               | 2        | 3.02                     | 36.22                    | 22.11                 | 23.39                       | 94.50%              |
| EX-3                               | 3        | 4.53                     | 54.33                    | 33.38                 | 35.09                       | 95.12%              |
| EX-4                               | 4        | 6.04                     | 72.44                    | 44.65                 | 46.78                       | 95.43%              |
| EX-5                               | 5        | 7.55                     | 90.55                    | 55.92                 | 58.48                       | 95.62%              |
| EX-6                               | 6        | 9.06                     | 108.66                   | 67.19                 | 70.18                       | 95.74%              |
| EX-7                               | 7        | 10.56                    | 126.77                   | 78.46                 | 81.87                       | 95.83%              |
| EX-8                               | 8        | 12.07                    | 144.88                   | 89.73                 | 93.57                       | 95.90%              |

| AquaCell Crates +<br>1 Side Plate | # Layers | Height of<br>layers (ft) | Height of<br>Layers (in) | Net Volume<br>water (ft³) | Gross Volume<br>total (ft³) | Percentage<br>water |
|-----------------------------------|----------|--------------------------|--------------------------|---------------------------|-----------------------------|---------------------|
| EX-1                              | 1        | 1.51                     | 18.11                    | 10.75                     | 11.70                       | 91.95%              |
| EX-2                              | 2        | 3.02                     | 36.22                    | 21.95                     | 23.39                       | 93.81%              |
| EX-3                              | 3        | 4.53                     | 54.33                    | 33.14                     | 35.09                       | 94.44%              |
| EX-4                              | 4        | 6.04                     | 72.44                    | 44.33                     | 46.78                       | 94.75%              |
| EX-5                              | 5        | 7.55                     | 90.55                    | 55.52                     | 58.48                       | 94.93%              |
| EX-6                              | 6        | 9.06                     | 108.66                   | 66.71                     | 70.18                       | 95.06%              |
| EX-7                              | 7        | 10.56                    | 126.77                   | 77.90                     | 81.87                       | 95.15%              |
| EX-8                              | 8        | 12.07                    | 144.88                   | 89.09                     | 93.57                       | 95.21%              |

| AquaCell Crates +<br>1 Side Plate | # Layers | Height of<br>layers (ft) | Height of<br>Layers (in) | Net Volume<br>water (ft³) | Gross Volume<br>total (ft³) | Percentage<br>water |
|-----------------------------------|----------|--------------------------|--------------------------|---------------------------|-----------------------------|---------------------|
| EX-1                              | 1        | 1.51                     | 18.11                    | 10.67                     | 11.70                       | 91.27%              |
| EX-2                              | 2        | 3.02                     | 36.22                    | 21.79                     | 23.39                       | 93.13%              |
| EX-3                              | 3        | 4.53                     | 54.33                    | 32.90                     | 35.09                       | 93.75%              |
| EX-4                              | 4        | 6.04                     | 72.44                    | 44.01                     | 46.78                       | 94.06%              |
| EX-5                              | 5        | 7.55                     | 90.55                    | 55.12                     | 58.48                       | 94.25%              |
| EX-6                              | 6        | 9.06                     | 108.66                   | 66.23                     | 70.18                       | 94.38%              |
| EX-7                              | 7        | 10.56                    | 126.77                   | 77.34                     | 81.87                       | 94.46%              |
| EX-8                              | 8        | 12.07                    | 144.88                   | 88.45                     | 93.57                       | 94.53%              |

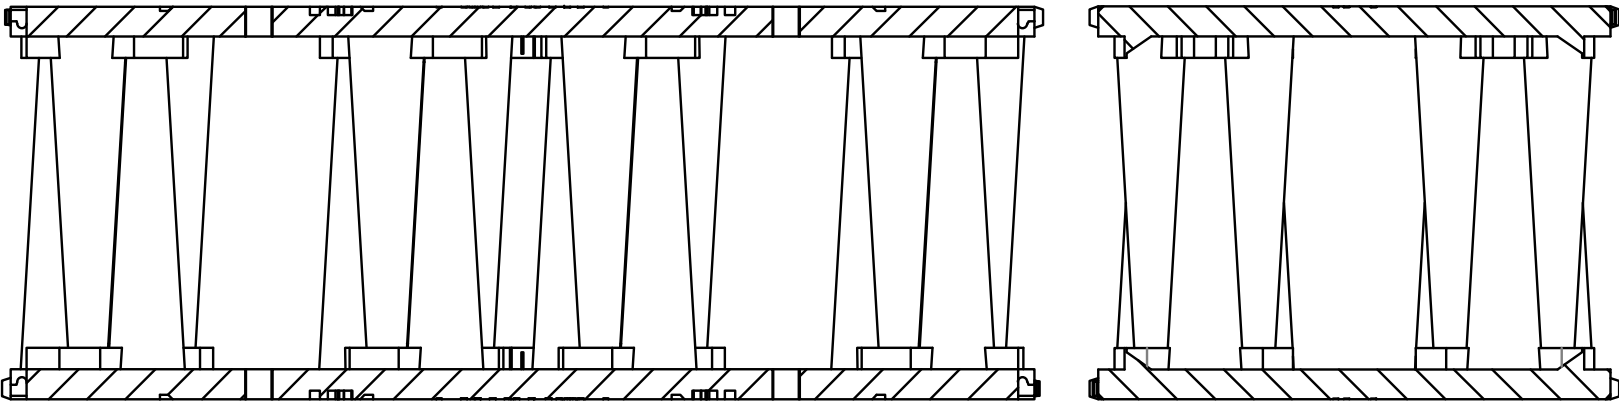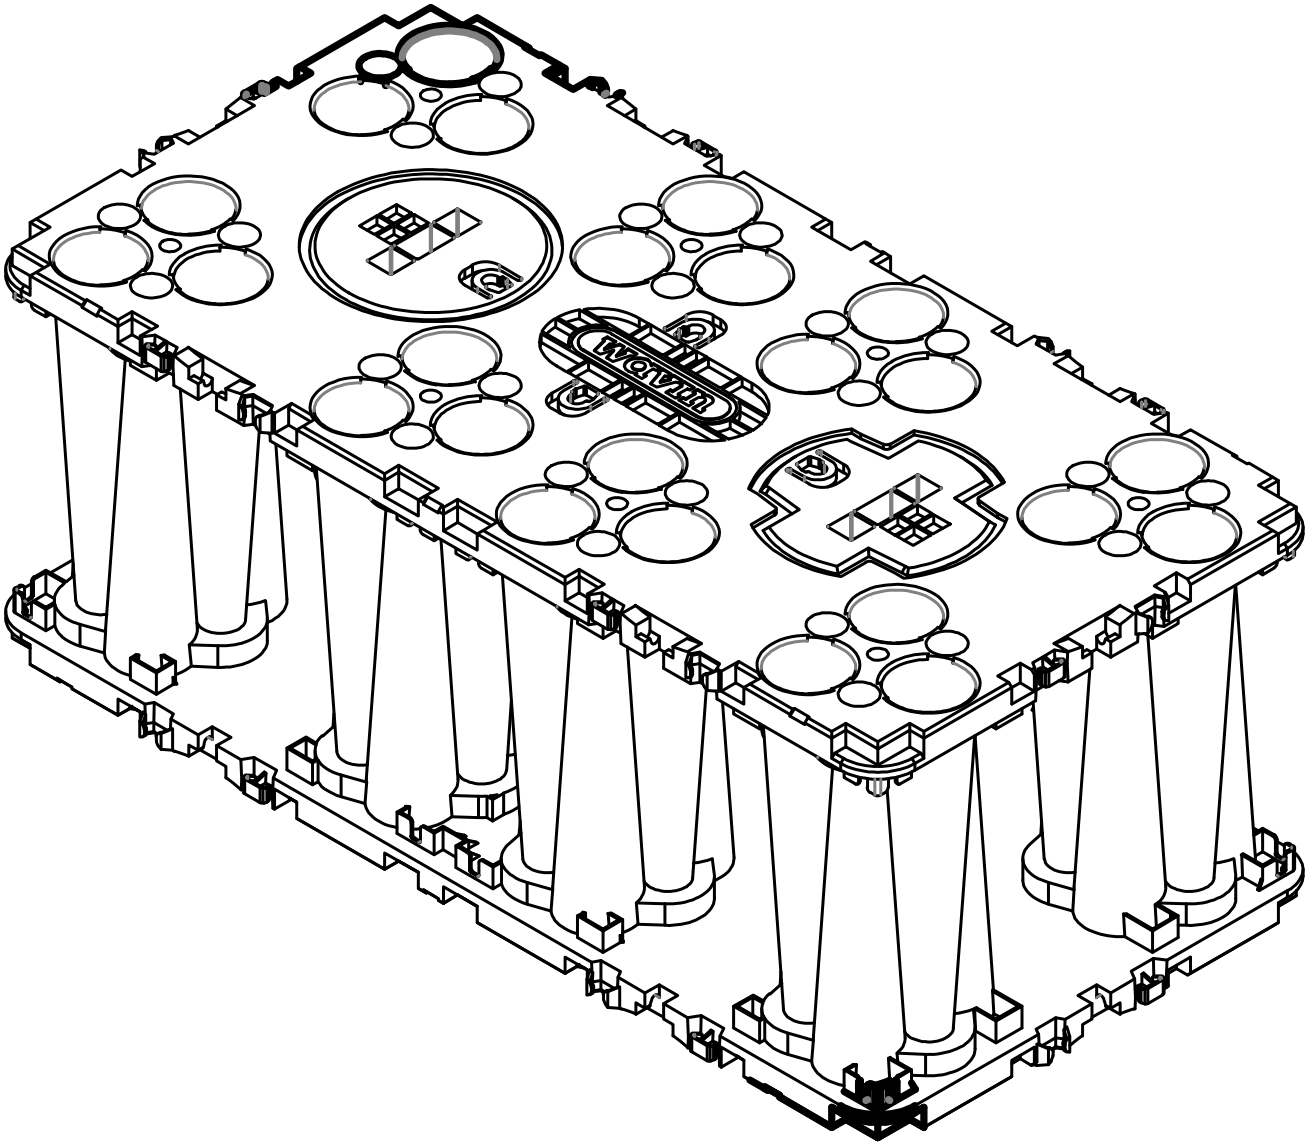

Managing water better since 1955.  
 950 Winter Street  
 Waltham, MA 02451  
 wavin.us.com  
 wavintechsupport@orbia.com

Title: AquaCell Volume Calculations - Extra Strong (EX) Configuration

|   |               |                 |                            |
|---|---------------|-----------------|----------------------------|
| The design details/specifications presented in this document are for informational & reference purposes only and are subject to change without notice. Responsibility for design of any AquaCell system rests solely with the original design engineer of record. For questions, contact: wavintechsupport@orbia.com. | Drawn by: HJD | Approved by: KS | Sheet <u>2</u> of <u>2</u> |
|   | Scale: NTS    | Revision: 4     |                            |
|   | AQ-200-01     | Date: 11/10/25  |                            |