


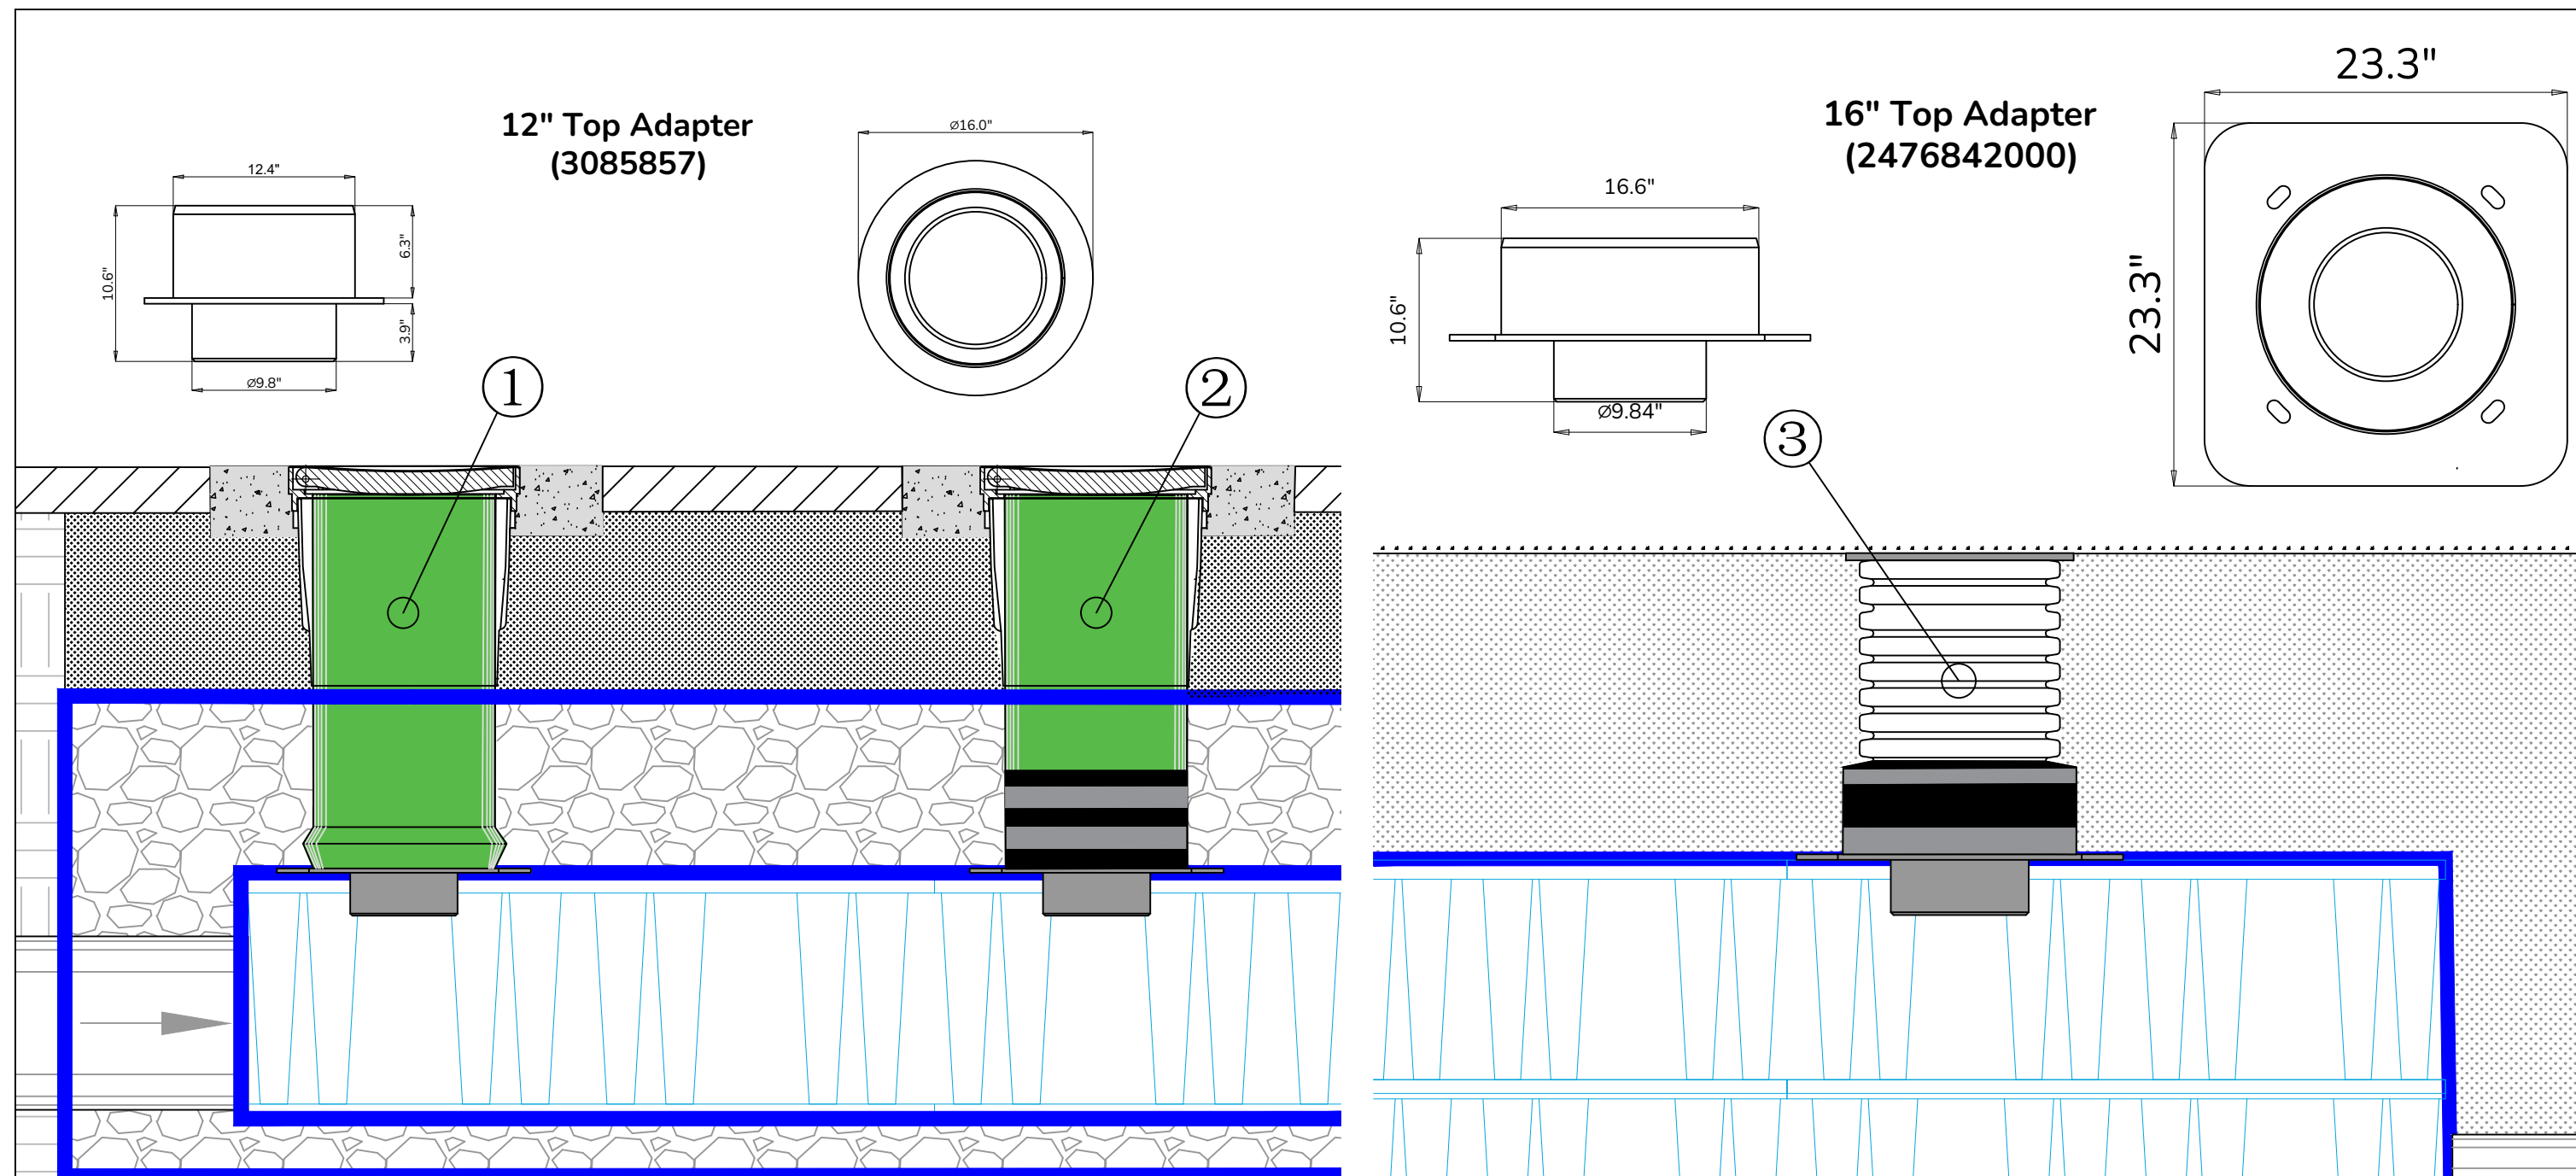

Notes:

12" | 16" Top Adapter (3085857 | 2476842000) available for installation of a vertical pipe for venting and/or inspection into **AquaCell** tank. All castings provided by **OTHERS**.

1. Install vertical **12" PVC SDR-35/26 GASKETED bell end pipe (ASTM D3034/ F477)** over riser of 12" Top Adapter (Traffic | Non-traffic).
2. Install vertical **12" PVC SDR-35/26 PLAIN end pipe (ASTM D3034)** over riser of 12" Top Adapter (Traffic | Non-traffic). Use 12" flexible coupler & stainless steel straps to secure pipe & adapter.
3. Install vertical **12" HDPE plain end pipe (ASTM F2306 | F2648)** in riser of 16" top adapter (**Non-traffic applications only**). Wrap fabric around 12" Top Adapter and wrap with corrosion-resistant tape
4. **Not Shown** - **18" SCH.40 plain end pipe w/ ID 16.81" (ASTM D2665)** over riser of **16" Top Adapter** (Traffic | Non-traffic).
5. Reference **AquaCell Installation Guide & AquaCell Compatible Pipe Connections (AQ-200-02)** for further information and instruction on vertical & lateral pipe connections.



Managing water better since 1955.

950 Winter Street
Waltham, MA 02451

wavin.us

wavintechsupport@orbia.com



The design details/specifications presented in this document are for informational purposes only and are subject to change without notice. Responsibility for design of any AquaCell system rests solely with the original design engineer of record. For questions, contact:
wavintechsupport@orbia.com

Title: AquaCell Top Adapter Connection Detail			
Date: 6/24/2025	Scale: NTS	Drawing: AQ-100-04	Rev: 3
Drawn: HJD	Approved: JS	Sheet: 1 of 1	