


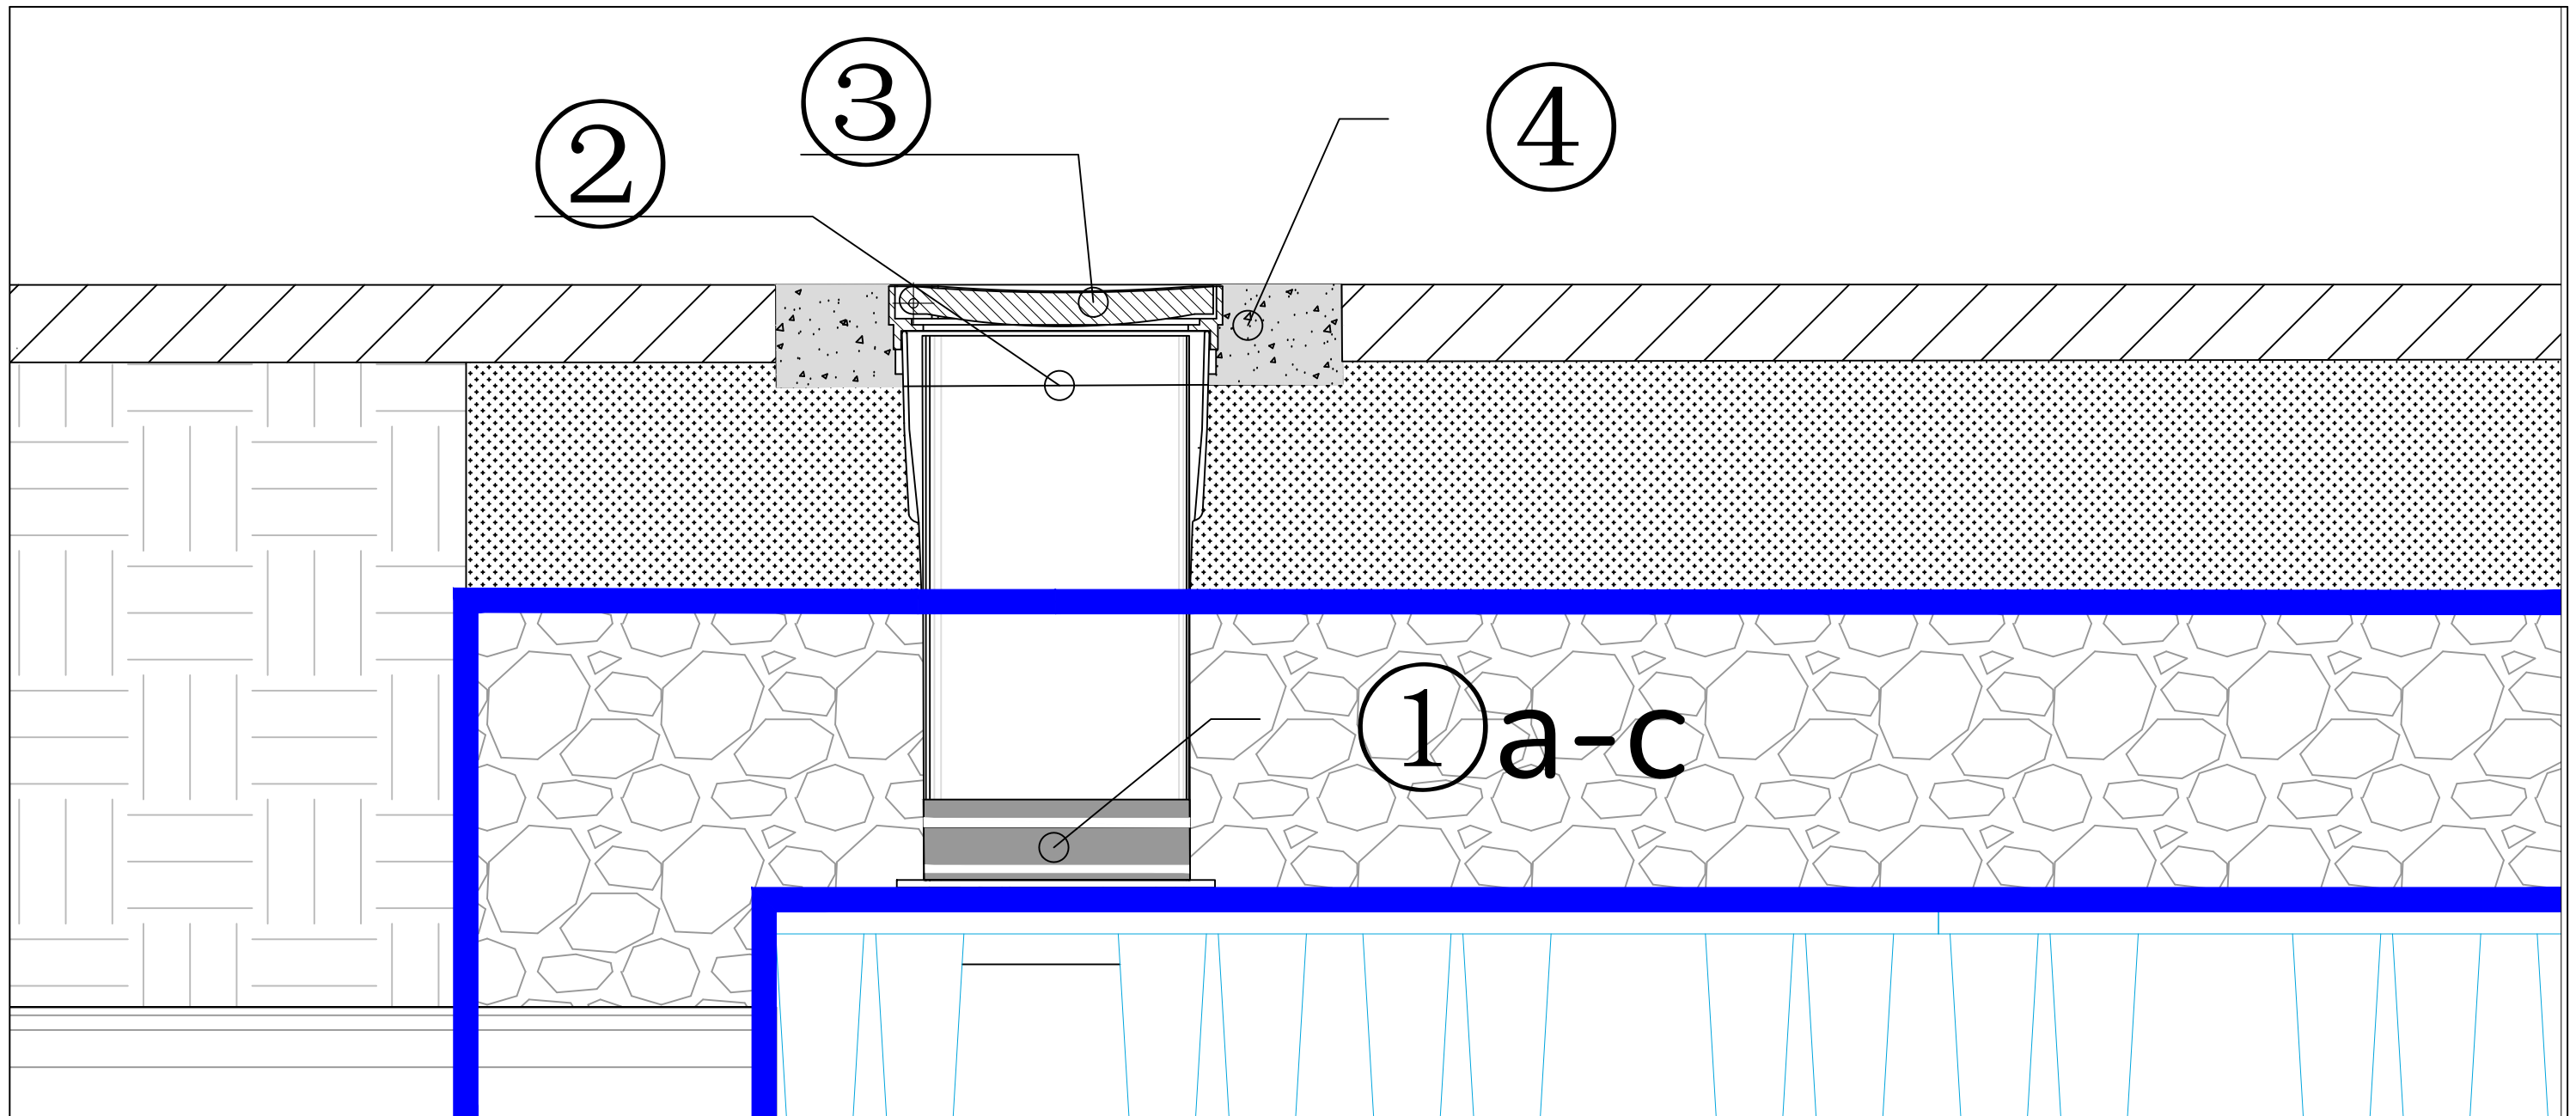

Notes:

1. For connection to **12" Top Adapter (3085857)**, use 12" PVC SDR-35 (ASTM D3034/ F477) gasketed bell end pipe for vertical connection to surface (**plain end shown**).
 - a. Locate cutout points at the top of the AquaCell system where the Top Adapter will be installed.
 - b. Cut the fabric on top and install the top adapter in previously cored 10" open hole, spigot -end first.
 - c. Once installed, secure the fabric around the top adapter & base of PVC riser with steel bands or appropriate corrosion resistant protection tape.
2. Install a PVC Inline Drain or similar coupler that transitions 12" PVC sewer pipe at surface to the appropriately sized frame/grate for the application (**Provided by others**).
3. Provide a frame/grate appropriate to the application that takes into account local traffic and soil conditions (**Provided by others**).
4. Concrete pad and asphalt to be installed on site for HS-20/25 installations (**Provided by others**). Sizing and depth of concrete pad determined by inline drain provider.



Managing water better since 1955.

950 Winter Street
Waltham, MA 02451

wavin.us

wavintechsupport@orbia.com



The design details/specifications presented in this document are for informational purposes only and are subject to change without notice. Responsibility for design of any AquaCell system rests solely with the original design engineer of record. For questions, contact: wavintechsupport@orbia.com

Title: AquaCell Vertical Riser Connection Detail (HS-20/25)

Date: 6/19/2025	Scale: NTS	Drawing: AQ-100-06	Rev: 2
Drawn: HJD	Approved: JS	Sheet: 1 of 1	