


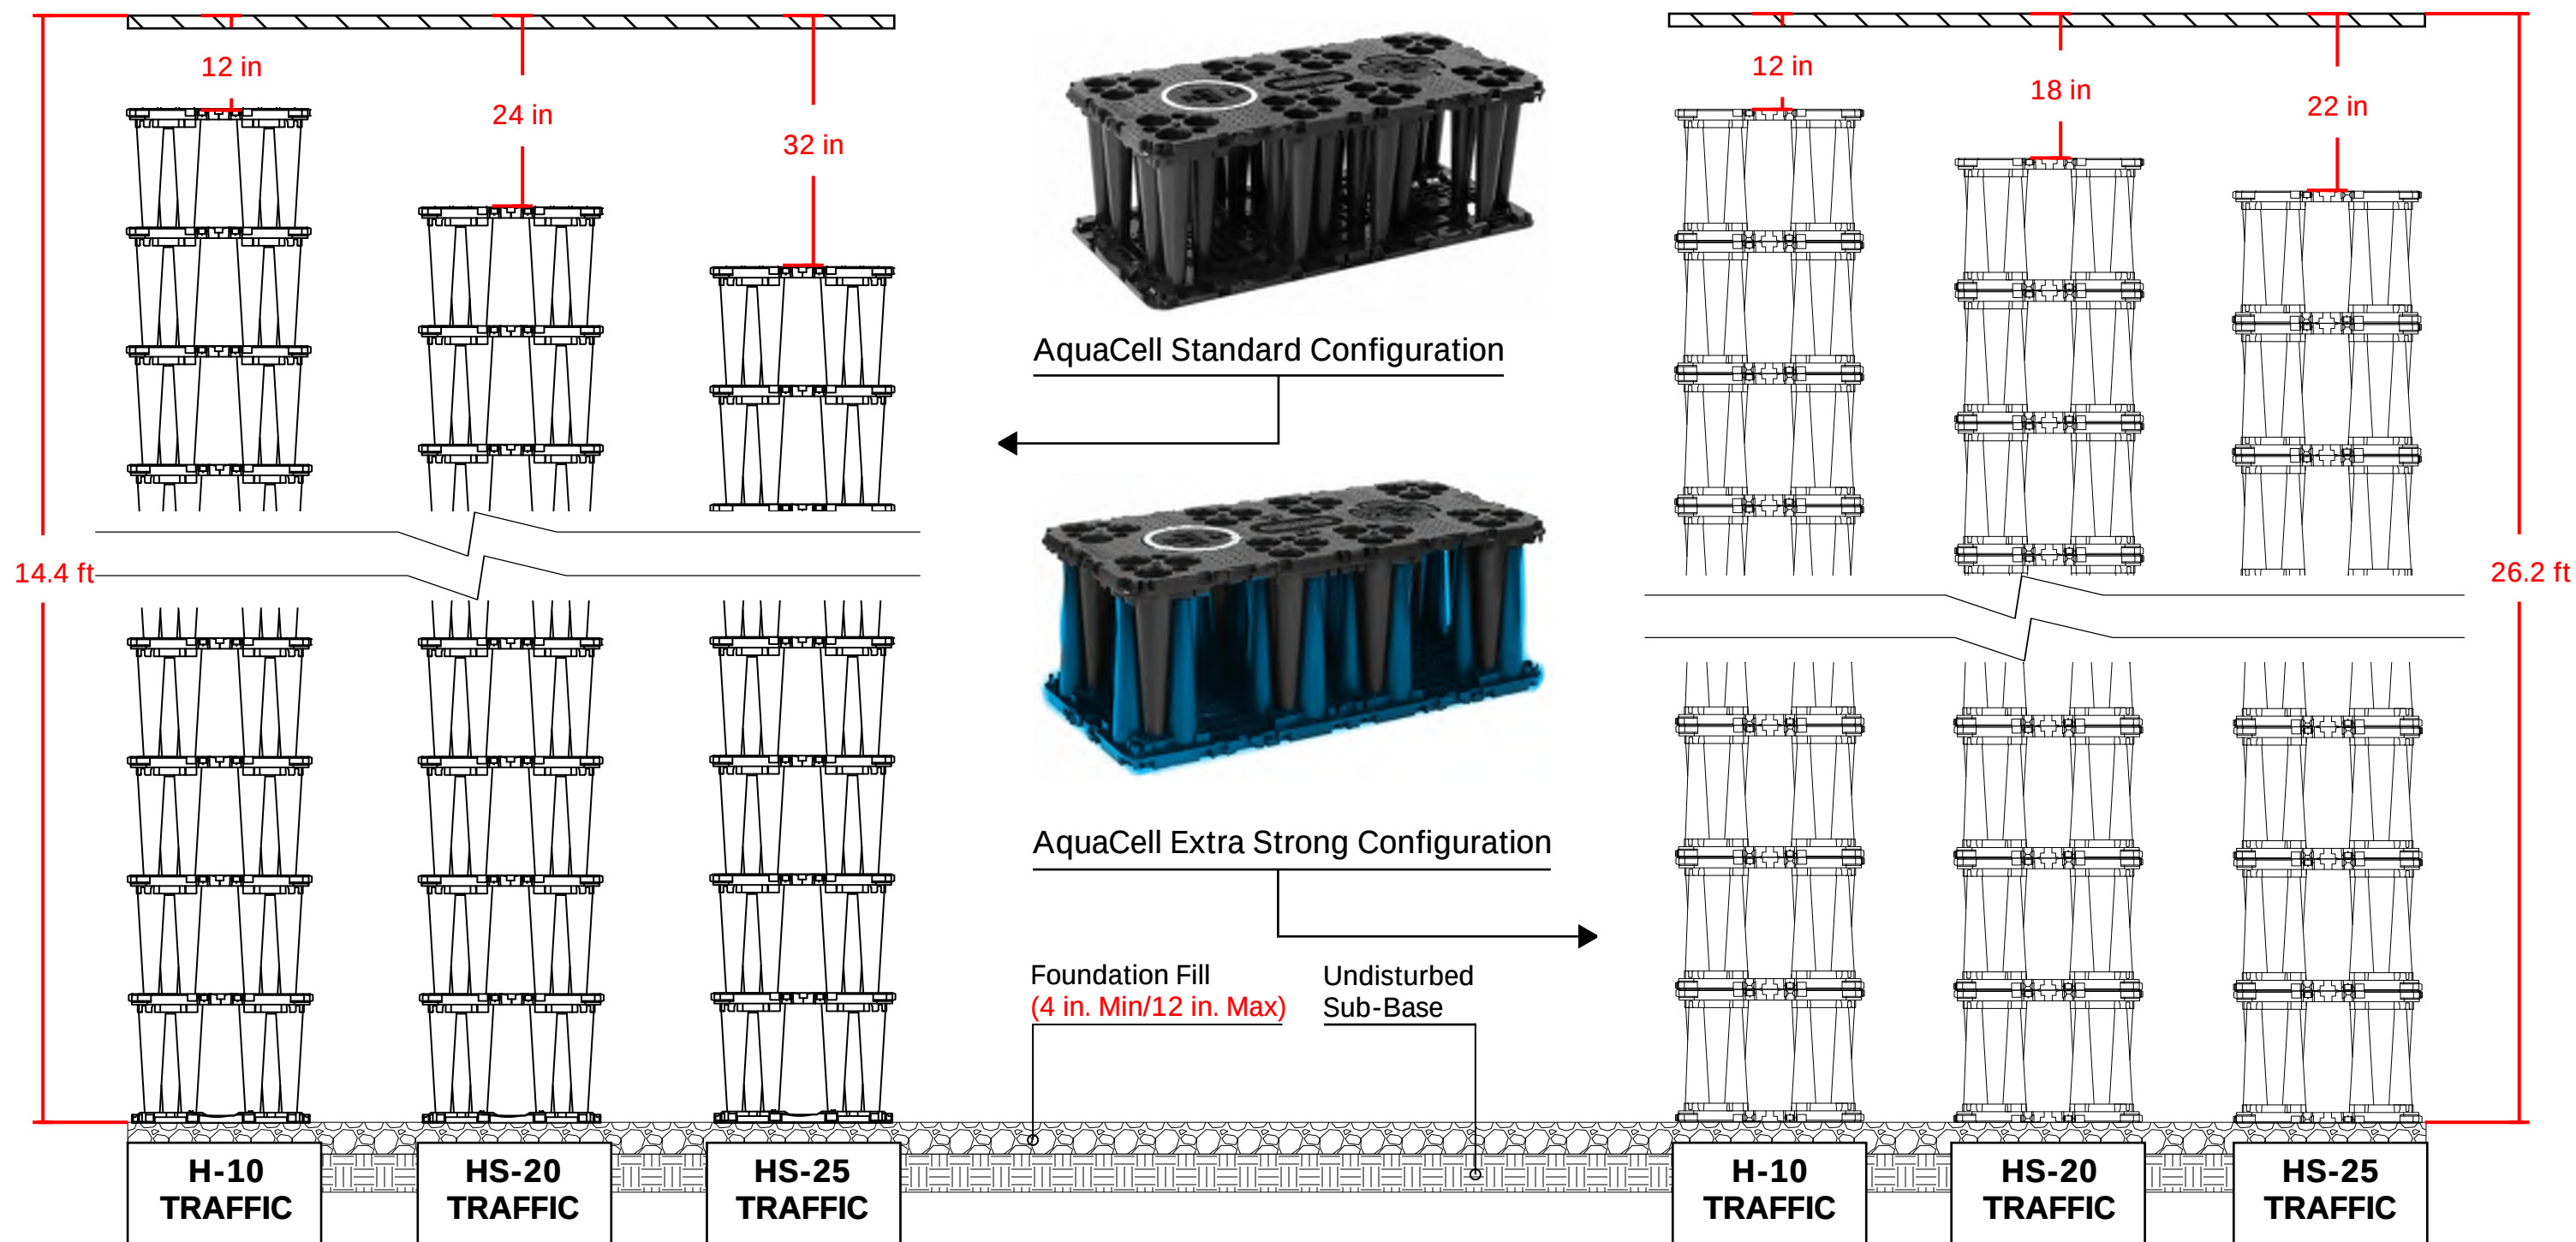

NOTES:

1. AquaCell units can be stacked to a maximum of eight (8) layers for an underground stormwater retention/detention system.
2. For a **single AquaCell Standard unit** meeting AASHTO HS-25, maximum burial depth is 14.1 feet below surface level. For **AquaCell Extra Strong unit** meeting AASHTO HS-25, maximum burial depth is 26.1 feet below surface level.
3. Reference **AquaCell Installation Guide** for further information and instructions related to installation depths.