
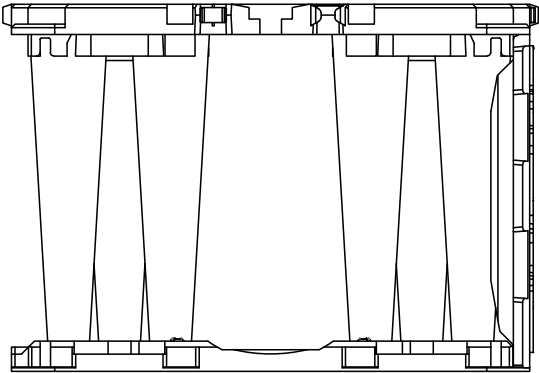
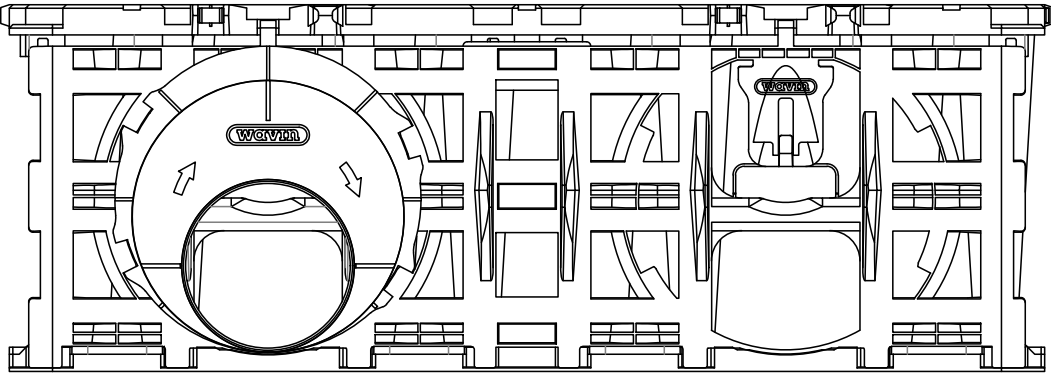


AquaCell Crate With Bottom Plate (1st Layer Only)	# Layers	Height of Layers (ft)	Height of Layers (in)	Water Volume (ft³)	Total Crate Volume (ft³)	Percentage Water
SC-1	1	1.39	16.73	10.25	10.81	94.87%
SC-2	2	2.71	32.48	20.0	20.98	95.33%
SC-3	3	4.02	48.23	29.7	31.15	95.49%
SC-4	4	5.33	63.98	39.5	41.32	95.57%
SC-5	5	6.64	79.72	49.2	51.49	95.62%
SC-6	6	7.96	95.47	59.0	61.66	95.65%
SC-7	7	9.27	111.22	68.7	71.83	95.67%
SC-8	8	10.58	126.97	78.5	82.00	95.69%

AquaCell Crate + Bottom +1 Side Plate	# Layers	Height of Layers (ft)	Height of Layers (in)	Water Volume (ft³)	Gross Volume total (ft³)	Percentage Water
SC-1	1	1.39	16.73	10.17	10.81	94.13%
SC-2	2	2.71	32.48	19.84	20.98	94.57%
SC-3	3	4.02	48.23	29.50	31.15	94.72%
SC-4	4	5.33	63.98	39.17	41.32	94.79%
SC-5	5	6.64	79.72	48.83	51.49	94.84%
SC-6	6	7.96	95.47	58.50	61.66	94.87%
SC-7	7	9.27	111.22	68.16	71.83	94.90%
SC-8	8	10.58	126.97	77.83	82.00	94.91%

AquaCell Crate + Bottom + 2 Side Plates	# Layers	Height of Layers (ft)	Height of Layers (in)	Water Volume (ft³)	Gross Volume total (ft³)	Percentage Water
SC-1	1	1.39	16.73	10.09	10.81	93.39%
SC-2	2	2.71	32.48	19.68	20.98	93.80%
SC-3	3	4.02	48.23	29.26	31.15	93.95%
SC-4	4	5.33	63.98	38.85	41.32	94.02%
SC-5	5	6.64	79.72	48.43	51.49	94.07%
SC-6	6	7.96	95.47	58.02	61.66	94.10%
SC-7	7	9.27	111.22	67.60	71.83	94.12%
SC-8	8	10.58	126.97	77.19	82.00	94.13%

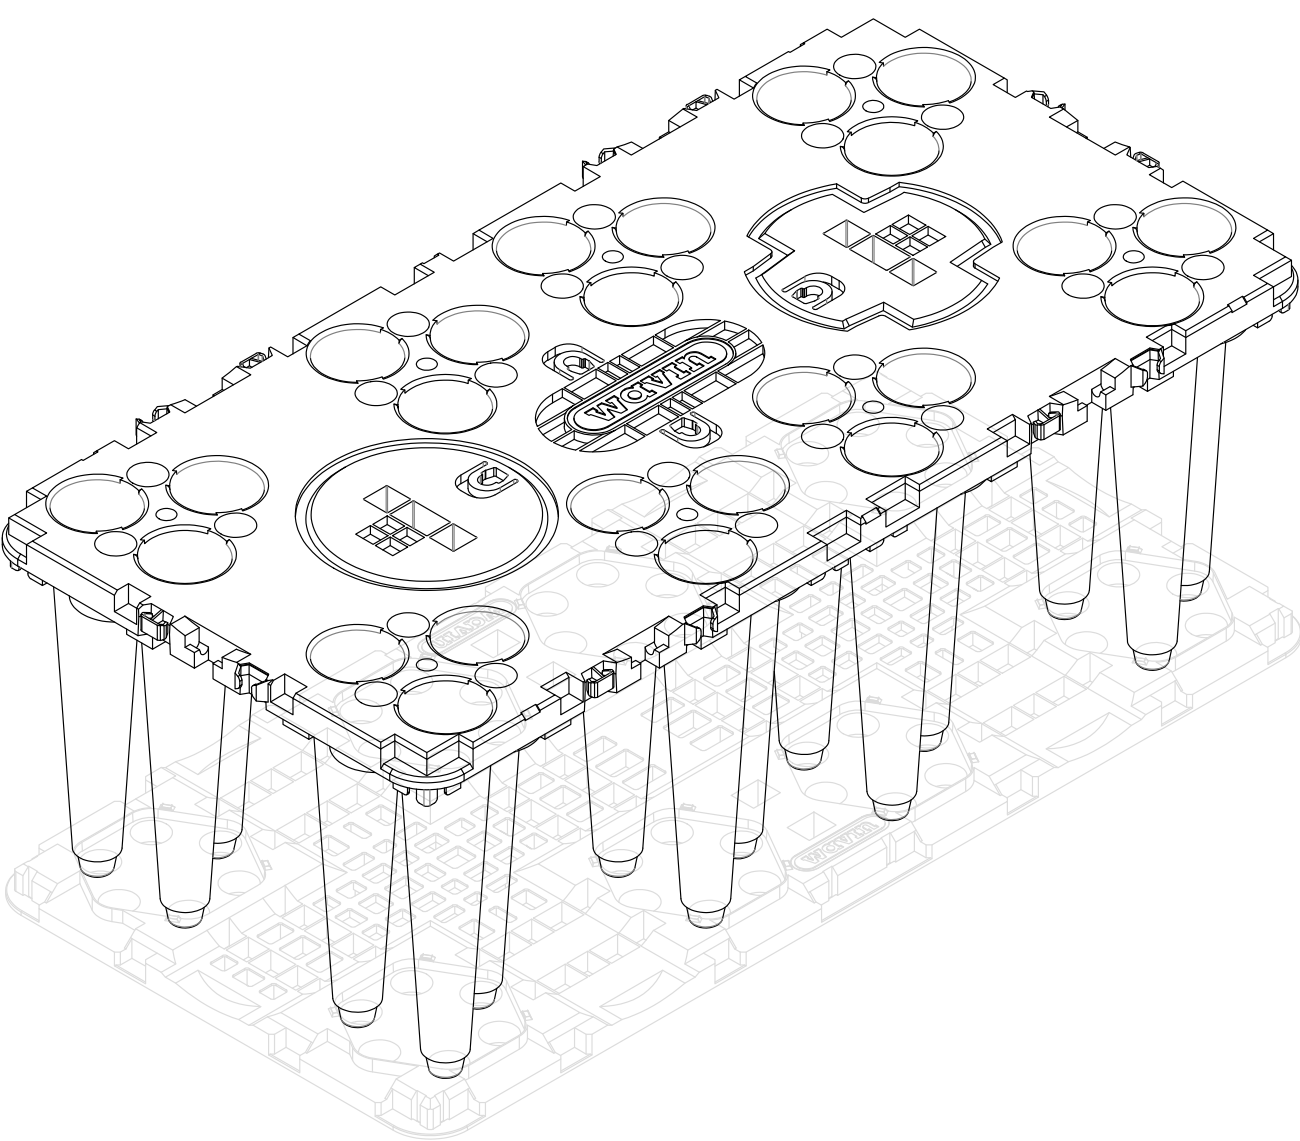

Managing water better since 1955.
950 Winter Street
Waltham, MA 02451
wavin.us.com
wavintechsupport@orbia.com

Title: AquaCell Volume Calculations - Standard (SC) Configuration

The design details/specifications presented in this document are for informational & reference purposes only and are subject to change without notice. Responsibility for design of any AquaCell system rests solely with the original design engineer of record. For questions, contact: wavintechsupport@orbia.com.



Drawn by: HJD
Scale: NTS
AQ-200-01

Approved by: KS
Revision: 4
Date: 11/10/25

AquaCell Crate + (2 Base Units)	# Layers	Height of layers (ft)	Height of Layers (in)	Water Volume (ft³)	Total Crate Volume (ft³)	Percentage water
EX-1	1	1.51	18.11	10.83	11.70	92.63%
EX-2	2	3.02	36.22	22.11	23.39	94.50%
EX-3	3	4.53	54.33	33.38	35.09	95.12%
EX-4	4	6.04	72.44	44.65	46.78	95.43%
EX-5	5	7.55	90.55	55.92	58.48	95.62%
EX-6	6	9.06	108.66	67.19	70.18	95.74%
EX-7	7	10.56	126.77	78.46	81.87	95.83%
EX-8	8	12.07	144.88	89.73	93.57	95.90%

AquaCell Crates + 1 Side Plate	# Layers	Height of layers (ft)	Height of Layers (in)	Net Volume water (ft³)	Gross Volume total (ft³)	Percentage water
EX-1	1	1.51	18.11	10.75	11.70	91.95%
EX-2	2	3.02	36.22	21.95	23.39	93.81%
EX-3	3	4.53	54.33	33.14	35.09	94.44%
EX-4	4	6.04	72.44	44.33	46.78	94.75%
EX-5	5	7.55	90.55	55.52	58.48	94.93%
EX-6	6	9.06	108.66	66.71	70.18	95.06%
EX-7	7	10.56	126.77	77.90	81.87	95.15%
EX-8	8	12.07	144.88	89.09	93.57	95.21%

AquaCell Crates + 2 Side Plate	# Layers	Height of layers (ft)	Height of Layers (in)	Net Volume water (ft³)	Gross Volume total (ft³)	Percentage water
EX-1	1	1.51	18.11	10.67	11.70	91.27%
EX-2	2	3.02	36.22	21.79	23.39	93.13%
EX-3	3	4.53	54.33	32.90	35.09	93.75%
EX-4	4	6.04	72.44	44.01	46.78	94.06%
EX-5	5	7.55	90.55	55.12	58.48	94.25%
EX-6	6	9.06	108.66	66.23	70.18	94.38%
EX-7	7	10.56	126.77	77.34	81.87	94.46%
EX-8	8	12.07	144.88	88.45	93.57	94.53%

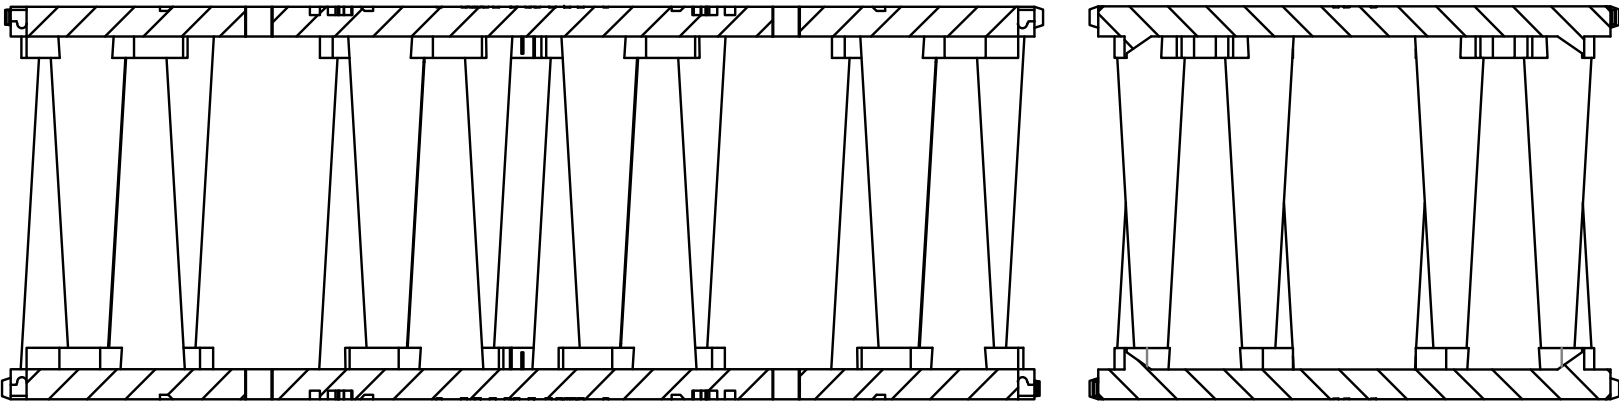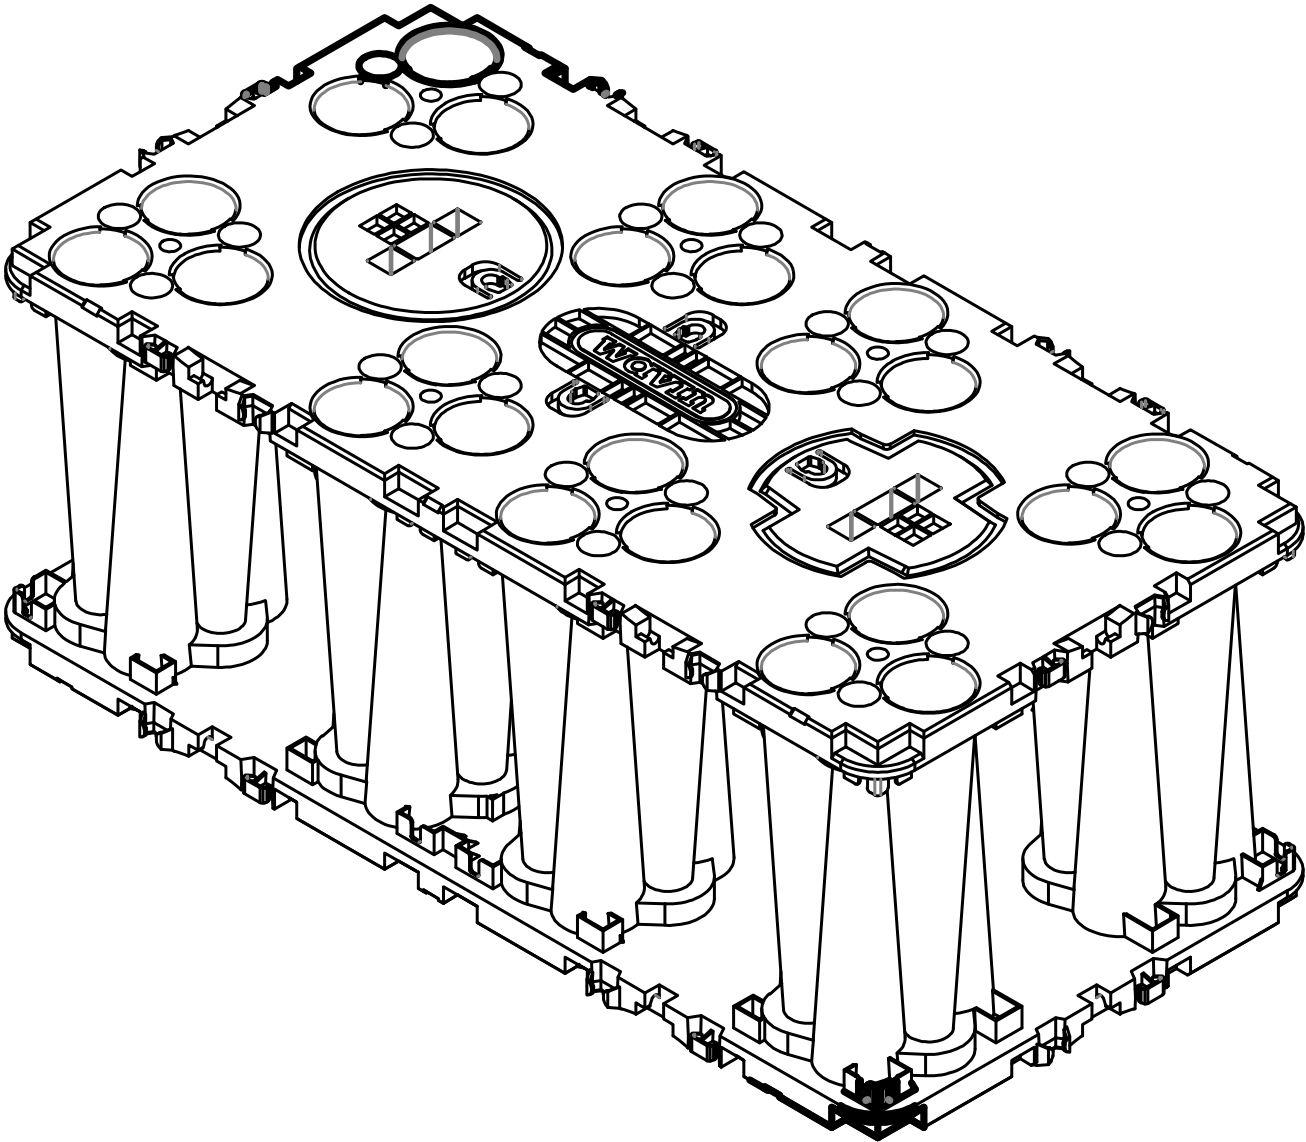

Managing water better since 1955.
 950 Winter Street
 Waltham, MA 02451
 wavin.us.com
 wavintechsupport@orbia.com

Title: AquaCell Volume Calculations - Extra Strong (EX) Configuration

The design details/specifications presented in this document are for informational & reference purposes only and are subject to change without notice. Responsibility for design of any AquaCell system rests solely with the original design engineer of record. For questions, contact: wavintechsupport@orbia.com.	Drawn by: HJD	Approved by: KS	Sheet <u>2</u> of <u>2</u>
	Scale: NTS	Revision: 4	
	AQ-200-01	Date: 11/10/25	