
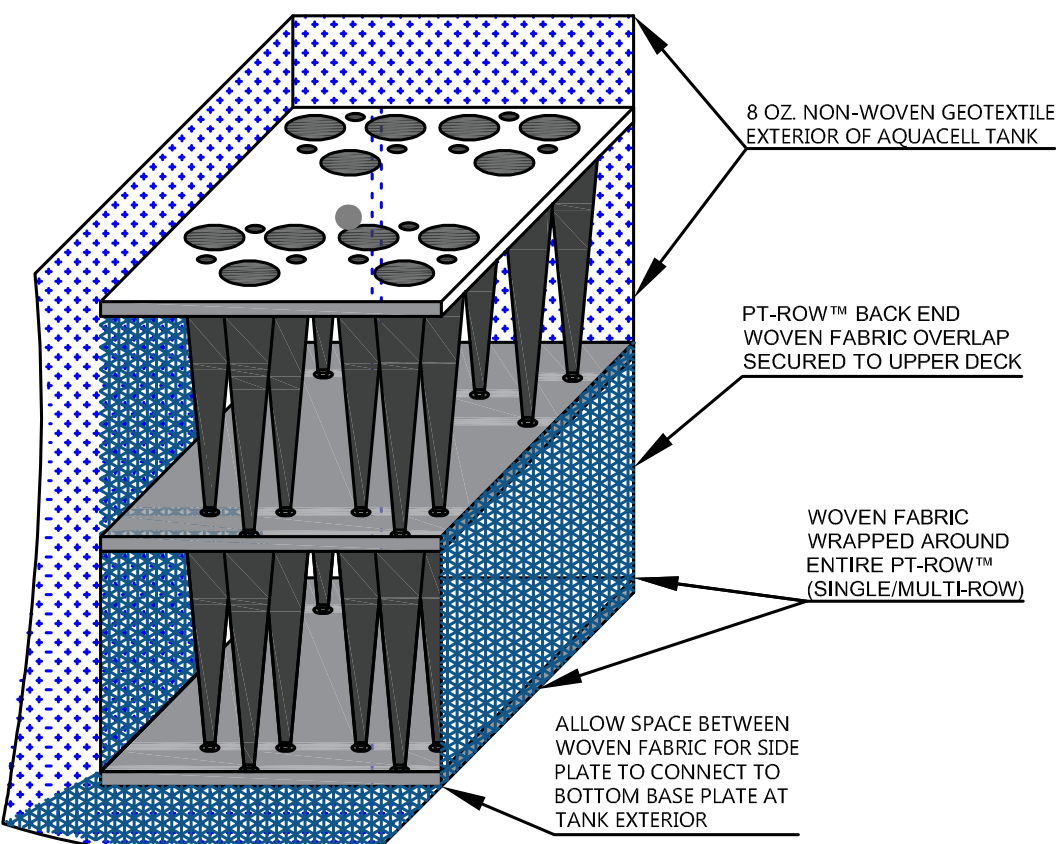


WAVIN PT-ROW™ (Pre-Treatment Row)

INTEGRATED TECHNOLOGIES
LOUAN TILLMAN
(615) 738-6217
TILLMANLOUAN@GMAIL.COM

- FABRIC PLACEMENT:** WOVEN MONOFILAMENT PP GEOTEXTILE FABRIC LAID ABOVE BASE LAYER OF NON-WOVEN GEOTEXTILE AND BELOW THE BOTTOM PLATES OF THE DESIGNATED **PT-ROW™** AREA.
 - EXTEND WOVEN FABRIC OUTWARD TO THE LENGTH AND WIDTH OF THE DESIGNED AREA (SINGLE OR MULTI-STACK).
 - ENSURE ENOUGH FABRIC IS EXTENDED BEYOND THE **PT-ROW™** AREA TO WRAP SIDE FABRIC TO THE TOP/ UPPER DECK OF CRATES. (18" FOR SINGLE LAYER, 36" FOR DOUBLE LAYER, 48" FOR TRIPLE LAYER).
- INSTALL BASE UNITS TO THE BOTTOM PLATES TO CREATE THE ROW / CHANNEL TO BE WRAPPED WITH WOVEN FABRIC.
- ONCE **PT-ROW™** CHANNEL IS BUILT, BRING WOVEN FABRIC LOCATED BELOW THE BOTTOM PLATES UP AND AROUND SIDES OF THE CRATE ROW.
 - TO SECURE THE WOVEN FABRIC TO THE **PT-ROW™**, FIND THE INTEGRATED SIDE PLATE SLOTS ON THE TOP DECK AND CUT THE FABRIC TO ENSURE A CLEAR OPENING TO INSTALL THE SIDE PLATE.
 - INSTALL THE SIDE PLATE BY SECURING THE HINGES IN THE TOP DECK AND LOWERING THE SIDE PLATE TO CONNECT TO THE BOTTOM PLATE CONNECTORS.
 - THE WOVEN FABRIC WILL BE SECURED BEHIND THE SIDE PLATES ALONG THE LENGTH OF THE DESIGNATED **PT-ROW™**.
- FOR DOUBLE & TRIPLE MULTI-STACK **PT-ROW™**, EXTEND AND CONNECT THE WOVEN FABRIC TO THE UPPERMOST TOP DECK AND SECURE THE FABRIC PER NOTE 3.
- AT THE BACK END OF THE **PT-ROW™**, PULL OVERLAP UP TO UPPER DECK AND SECURE PER NOTE 3.
- INSPECTION / MAINTENANCE CLEANOUTS TO BE LOCATED ABOVE **PT-ROW™** LOCATIONS.
 - CLEANOUTS RECOMMENDED EVERY 50' TO 100' (MINIMUM ONE AT BEGINNING OF EACH **PT-ROW™**).
- PT-ROW™** DETAILS SHOWN FOR EXAMPLE ONLY. EXACT DIMENSIONS OF **PT-ROW™** TO BE DETERMINED BY E.O.R.
 - REFERENCE **WAVIN AQUACELL PT-ROW™ SIZING AND DESIGN GUIDANCE** DOCUMENT FOR ADDITIONAL INFORMATION.
 - REFERENCE **AQUACELL INSTALLATION GUIDE** AND **AQUACELL O&M MANUAL** FOR INFORMATION ON CLEANING & MAINTENANCE OF **PT-ROW™**.

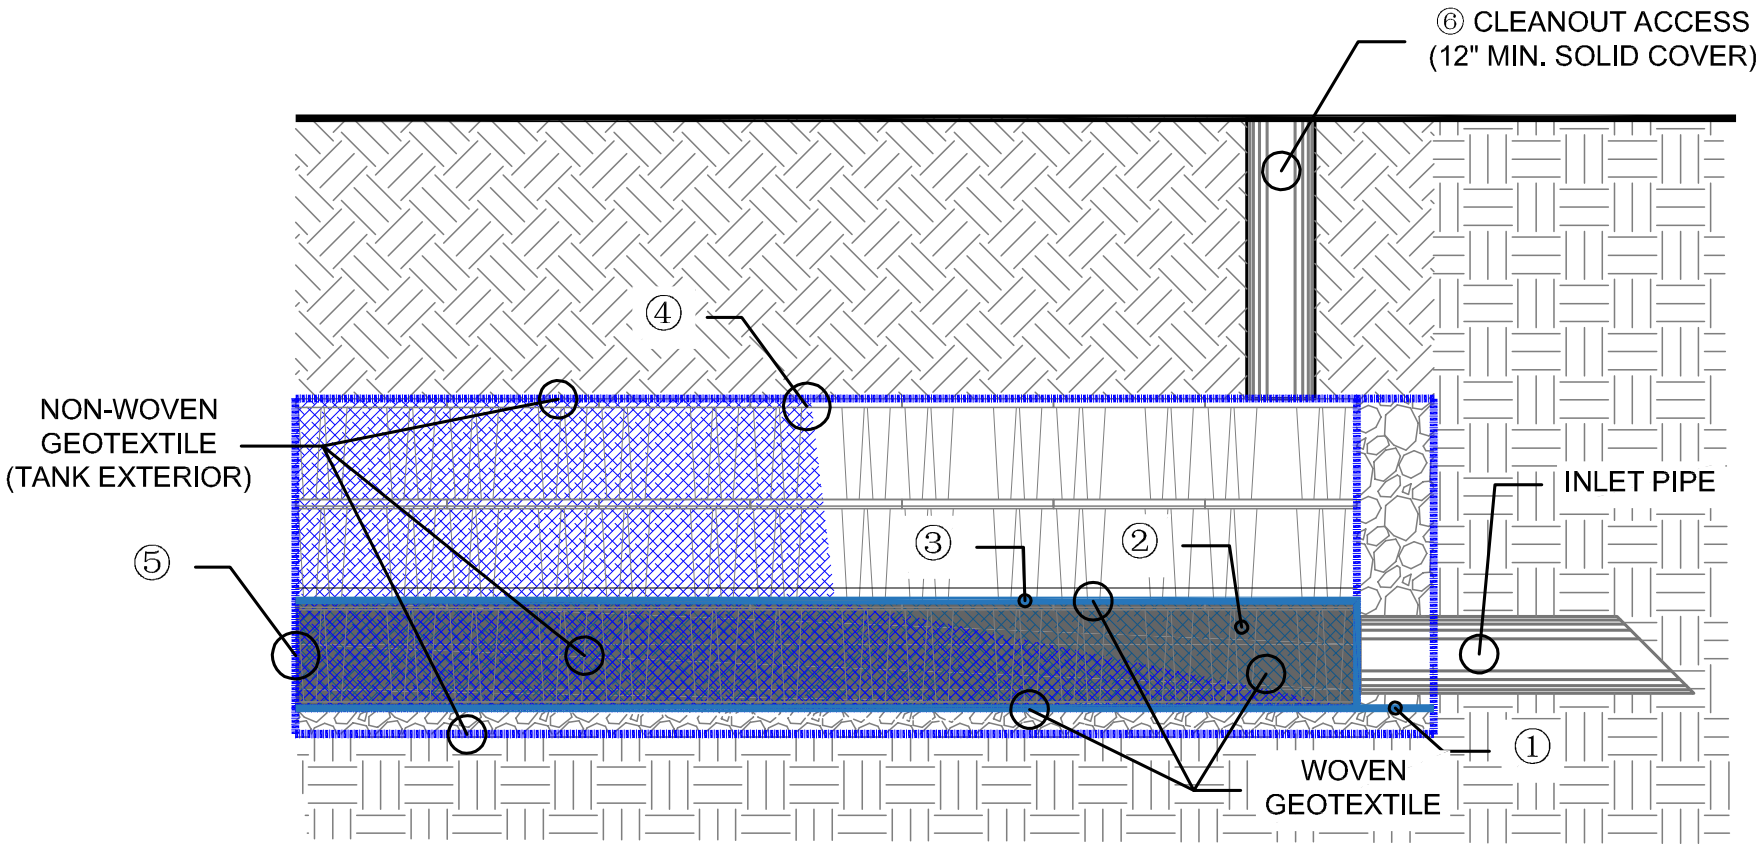

Managing water better since 1955.
950 Winter Street
Waltham, MA 02451
wavin.us
wavintechsupport@orbia.com



The design details/specifications presented in this document are for informational purposes only and are subject to change without notice. Responsibility for design of any AquaCell system rests solely with the original design engineer of record. For questions, contact: wavintechsupport@orbia.com

Title: AquaCell PT-ROW™ INSTALLATION GUIDANCE			
Date: 9/5/2025	Scale: NTS	Rev: 3	
Drawn: HJD	Approved:	Drawing: AQ-100-25	