


AquaCell Crate With Bottom Plate (1st Layer Only)	# Layers	Height of Layers (ft)	Height of Layers (in)	Water Volume (ft³)	Total Crate Volume (ft³)	Percentage Water
SC-1	1	1.39	16.73	10.25	10.81	94.87%
SC-2	2	2.71	32.48	20.0	20.98	95.33%
SC-3	3	4.02	48.23	29.7	31.15	95.49%
SC-4	4	5.33	63.98	39.5	41.32	95.57%
SC-5	5	6.64	79.72	49.2	51.49	95.62%
SC-6	6	7.96	95.47	59.0	61.66	95.65%
SC-7	7	9.27	111.22	68.7	71.83	95.67%
SC-8	8	10.58	126.97	78.5	82.00	95.69%

AquaCell Crate + Bottom +1 Side Plate	# Layers	Height of Layers (ft)	Height of Layers (in)	Water Volume (ft³)	Gross Volume total (ft³)	Percentage Water
SC-1	1	1.39	16.73	10.17	10.81	94.13%
SC-2	2	2.71	32.48	19.84	20.98	94.57%
SC-3	3	4.02	48.23	29.50	31.15	94.72%
SC-4	4	5.33	63.98	39.17	41.32	94.79%
SC-5	5	6.64	79.72	48.83	51.49	94.84%
SC-6	6	7.96	95.47	58.50	61.66	94.87%
SC-7	7	9.27	111.22	68.16	71.83	94.90%
SC-8	8	10.58	126.97	77.83	82.00	94.91%

AquaCell Crate + Bottom + 2 Side Plates	# Layers	Height of Layers (ft)	Height of Layers (in)	Water Volume (ft³)	Gross Volume total (ft³)	Percentage Water
SC-1	1	1.39	16.73	10.09	10.81	93.39%
SC-2	2	2.71	32.48	19.68	20.98	93.80%
SC-3	3	4.02	48.23	29.26	31.15	93.95%
SC-4	4	5.33	63.98	38.85	41.32	94.02%
SC-5	5	6.64	79.72	48.43	51.49	94.07%
SC-6	6	7.96	95.47	58.02	61.66	94.10%
SC-7	7	9.27	111.22	67.60	71.83	94.12%
SC-8	8	10.58	126.97	77.19	82.00	94.13%

INTEGRATED TECHNOLOGIES
 LOUAN TILLMAN
 (615) 738-6217
 TILLMANLOUAN@GMAIL.COM

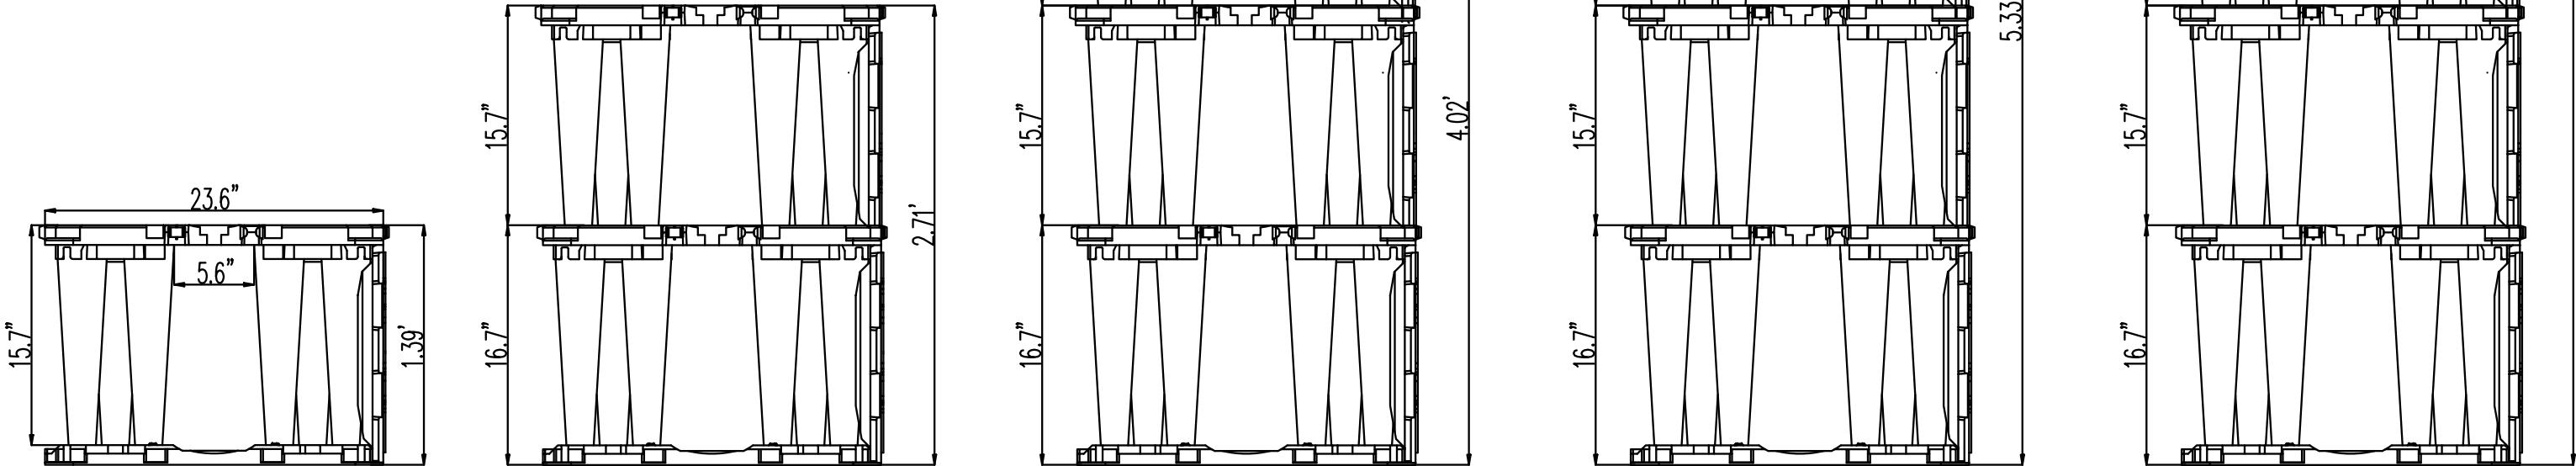

*maximum total of 8 layers stacked

NOTES:

1. Volume of designed water storage is an average of 95% of total volume of water stored within the AquaCell units
2. AquaCell units can be stacked to a maximum of eight (8) layers for an underground stormwater retention / detention system.
3. Water storage values shown represent one type of configuration. Additional side plates added will reduce percentage of water volume by an average of -.8% per layer.
4. Extra Strong AquaCell configuration (2 base units set within each other) has a water volume of 11.7 ft³ with 10.8 ft³ of designed water storage.



Managing water better since 1955.
 950 Winter Street
 Waltham, MA 02451
 wavin.us.com
 wavintechsupport@orbia.com

Title: AquaCell 5-Layer Stack w. Measurements

The design details/specifications presented in this document are for informational & reference purposes only and are subject to change without notice. Responsibility for design of any AquaCell system rests solely with the original design engineer of record. For questions, contact: wavintechsupport@orbia.com.

Drawn by: HJD
 Scale: 1:11
 AQ-100-05

Approved by: KS
 Revision: 2
 Date: 2/23/2025